
東京タワー / 基座平面図

LANDMARK-R11 | A3 | 1:500 | 単位 mm | 外観模式図

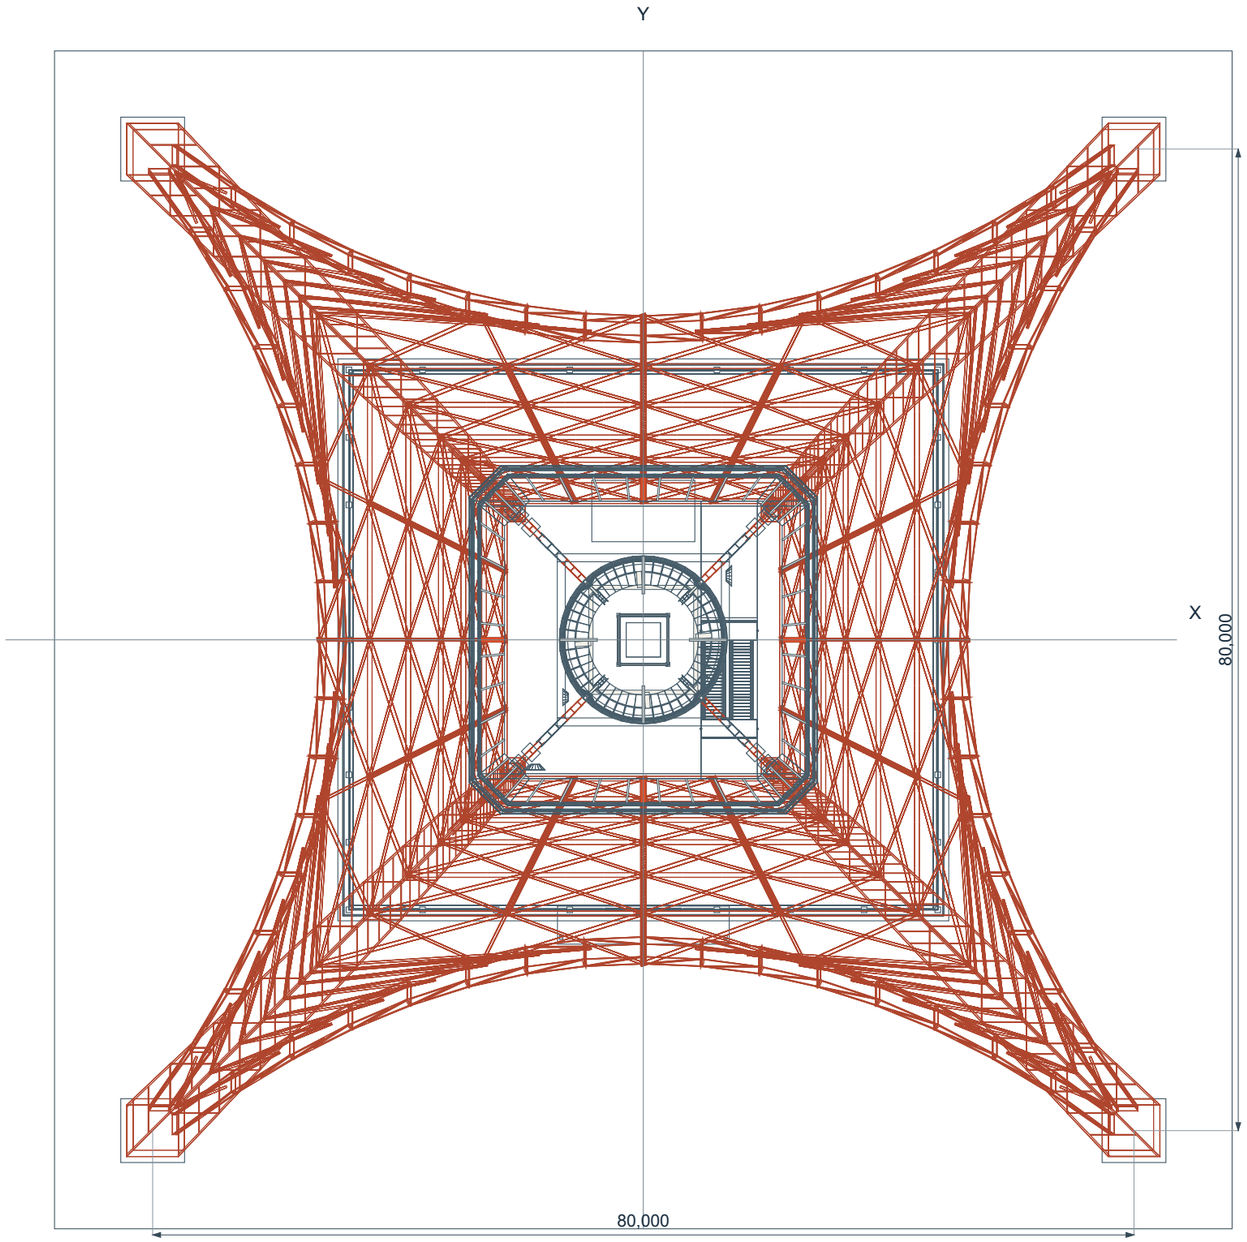

基座・足元 / 上部の投影外形を重ねた模式配置

方位はモデル軸のみ。実際の敷地方位・配置とは異なります。

公表値を参照 / 未測量・未計算 / NOT FOR CONSTRUCTION

モデル寸法と図面の対応

01 公式案内の公表値

全高 333,000 mm

メインデッキ150 m / トップデッキ250 m

02 歴史図の層別寸法と施工GL

JAEE復刻p97 Fig.3 / 1962年原論文

H11 27×27 m / H12 28×28 m

H13 29×24 m：歴史の独立平面を別記。

機能・現外装との対応は未確認。

トップ：円形 D13,000 mm（歴史図）

床モデル 120,000 / 125,000 mm

上部モデル 223,550 mm（H23帯）

公式案内値との換算・完成面実測ではない。

塔脚基準軸線間80,000 mmは図1参照。

床・外形の現況対応、部材・接合は仮定。

R11主脚・アーチは一体の組立材。

GL80–120m：下方と同じ4列の交差格子。

断面・板厚・割付は写真近似、未実測。

上部輪郭GL130,000–223,550は局所平滑近似。

足元建物の外形・階高・外装もモデル仮定。

03 座標とデータ

CADモデル空間は実寸1:1、単位mm。

平面はX/Y、立面はX/Zの正投影。

方位はモデル用。測量方位は未設定。

基座平面は上部投影外形も重ねて表示。

文字・寸法はDXFで編集可能。

04 参照資料（2026-11-01）

JAEE実在建物の振動性状 / 歴史図復刻

宮地技報 No18 p86 / No28 p65–66


tokyotower.co.jp/guidance/

観光床の完成面・現況構造は未測量。

text-CAD | LANDMARK-R11 | 2026-11-04

東京タワー / 正立面図

LANDMARK-R11 | A3 | 1:1500 | 単位 mm | 外観模式図

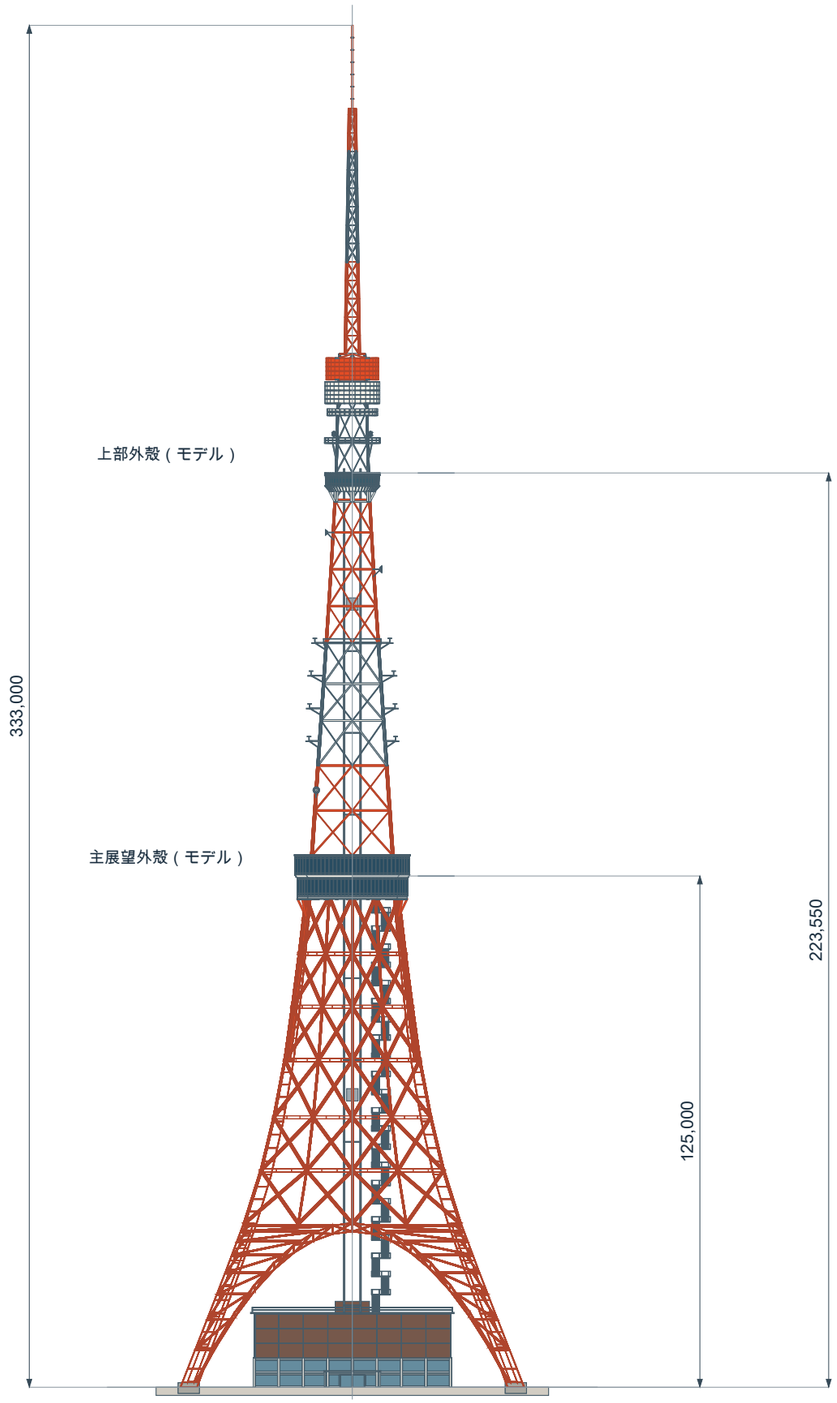

基準 GL ±0

正投影 / 展望施設の形状・鉄骨径は模式表現

公表値を参照 / 未測量・未計算 / NOT FOR CONSTRUCTION

モデル寸法と図面の対応

01 公式案内: メイン150 m / トップ250 m


施工GL: 主床 120,000/125,000・H23屋根 223,550 mm

公式案内値との換算・完成面実測ではない。

JAEE歴史H13 29×24 m：独立平面を別記。


現外装との対応未確認。部材・接合は仮定。

02 メインデッキ付近 / 1:300

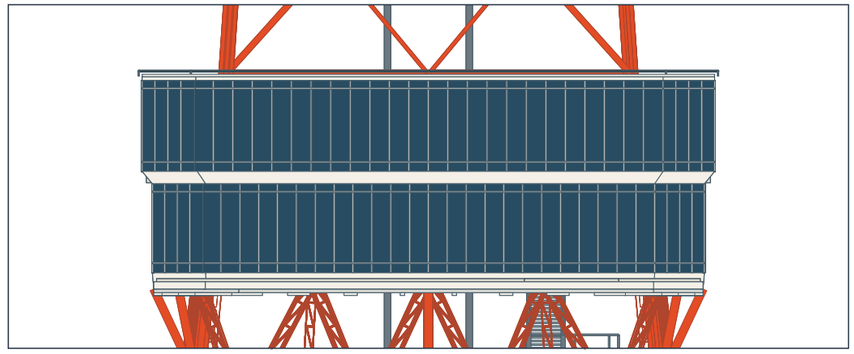

JAEE復刻p97 Fig.3：H11 27×27 / H12 28×28 m

03 円形展望台・H24 / 1:400

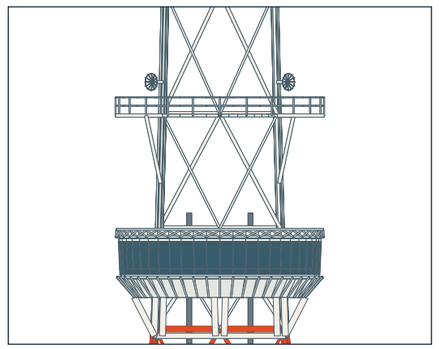


H23屋根GL223,550 / 円径13,000

SG外周補強 / ST支柱□450

宮地技報 No28 p65–66 / 改修参照

04 SG・ST / 1:1250

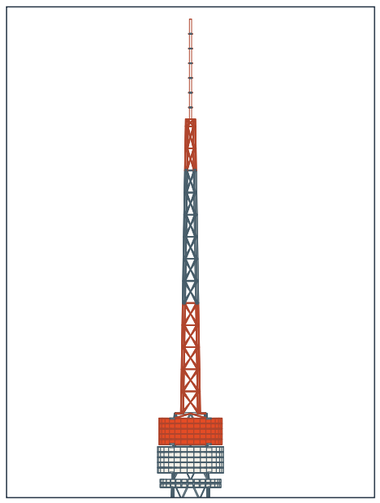


text-CAD | LANDMARK-R11 | 2026-11-04

東京タワー / 鋼接合部・節点詳細


LANDMARK-R11 | A3 | モデル空間 1:1 | 単位 mm | 外観模式図

公表値: 全高333,000 mm・公式案内150/250 m / モデル外殻125/223.55 mは解釈配置（完成面未測量）。

節点位置 / 下部〜主展望台 / 1:1000

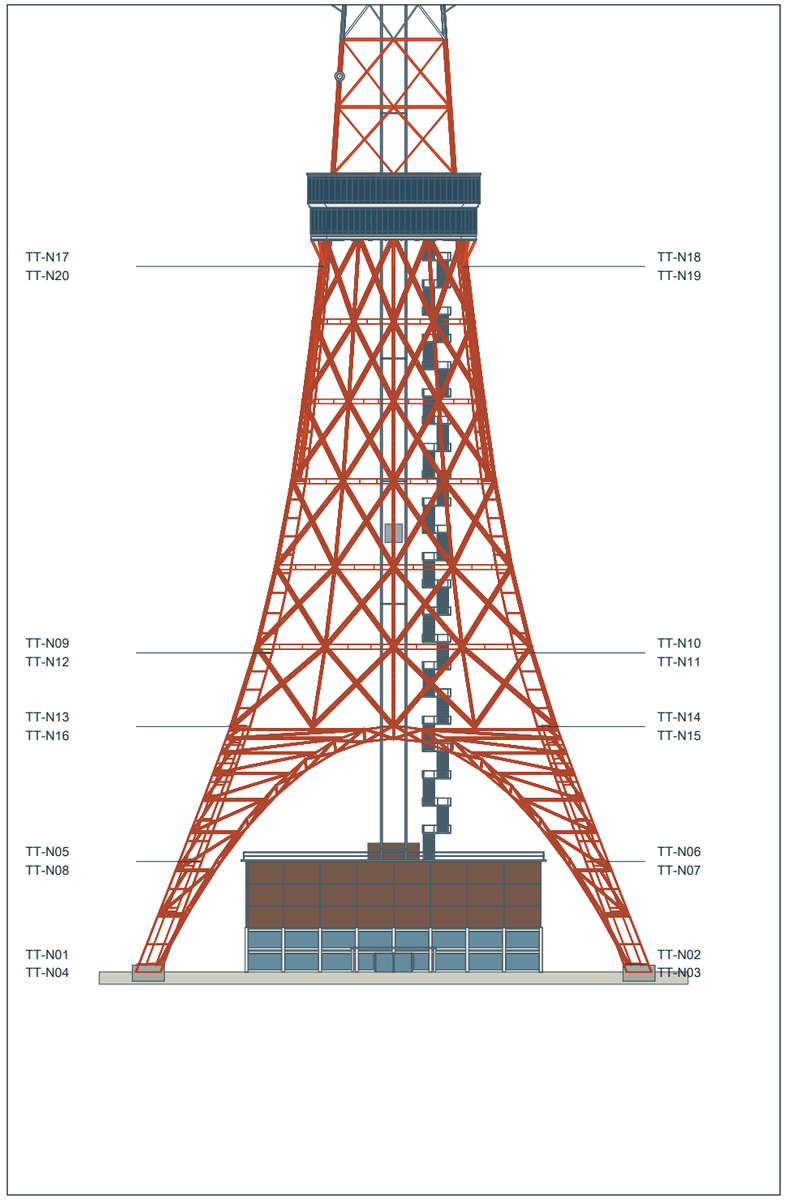


TT-N01 塔脚板組 1 / 1:20

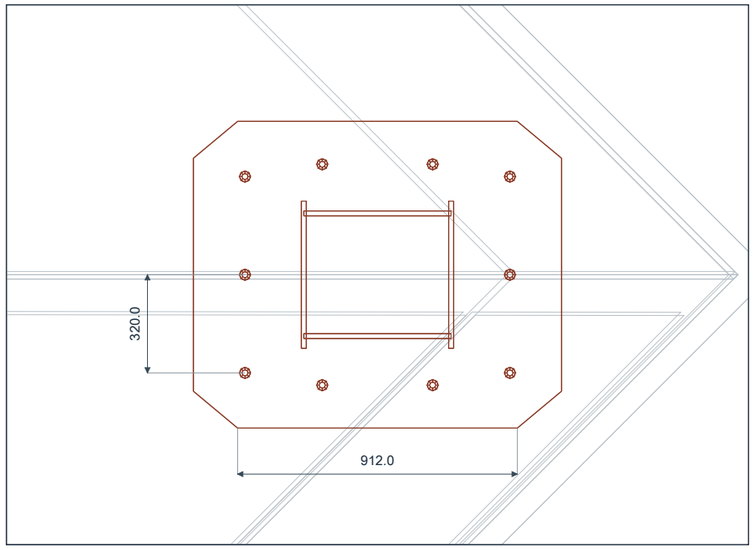

板厚 t=30 mm / 板幅・心々寸法 mm / 全て仮定

TT-N05 下部集合節点 1 / 1:20

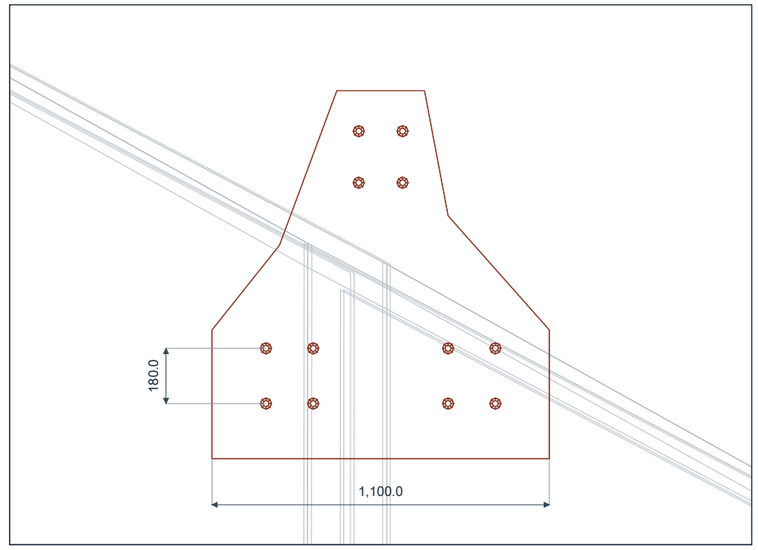


板厚 t=20 mm / 板幅・心々寸法 mm / 全て仮定

TT-N13 主材両面継手 1 / 1:20



板厚 t=16 mm / 板幅・心々寸法 mm / 全て仮定

TT-N17 主展望台支持節点 1 / 1:20

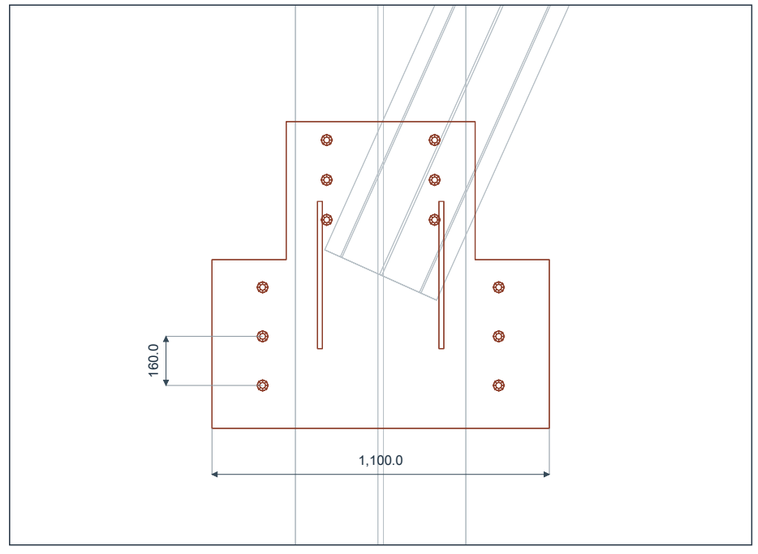

板厚 t=24 mm / 板幅・心々寸法 mm / 全て仮定

板面の正投影。板厚は注記、板幅とリベット心々は実寸の編集可能な寸法。

未測量・未計算 / NOT FOR CONSTRUCTION / 原建物の接合詳細ではありません。