
瀬戸大橋 / 南北備讃瀬戸大橋

橋梁全体平面図 / 橋軸X・横断Y

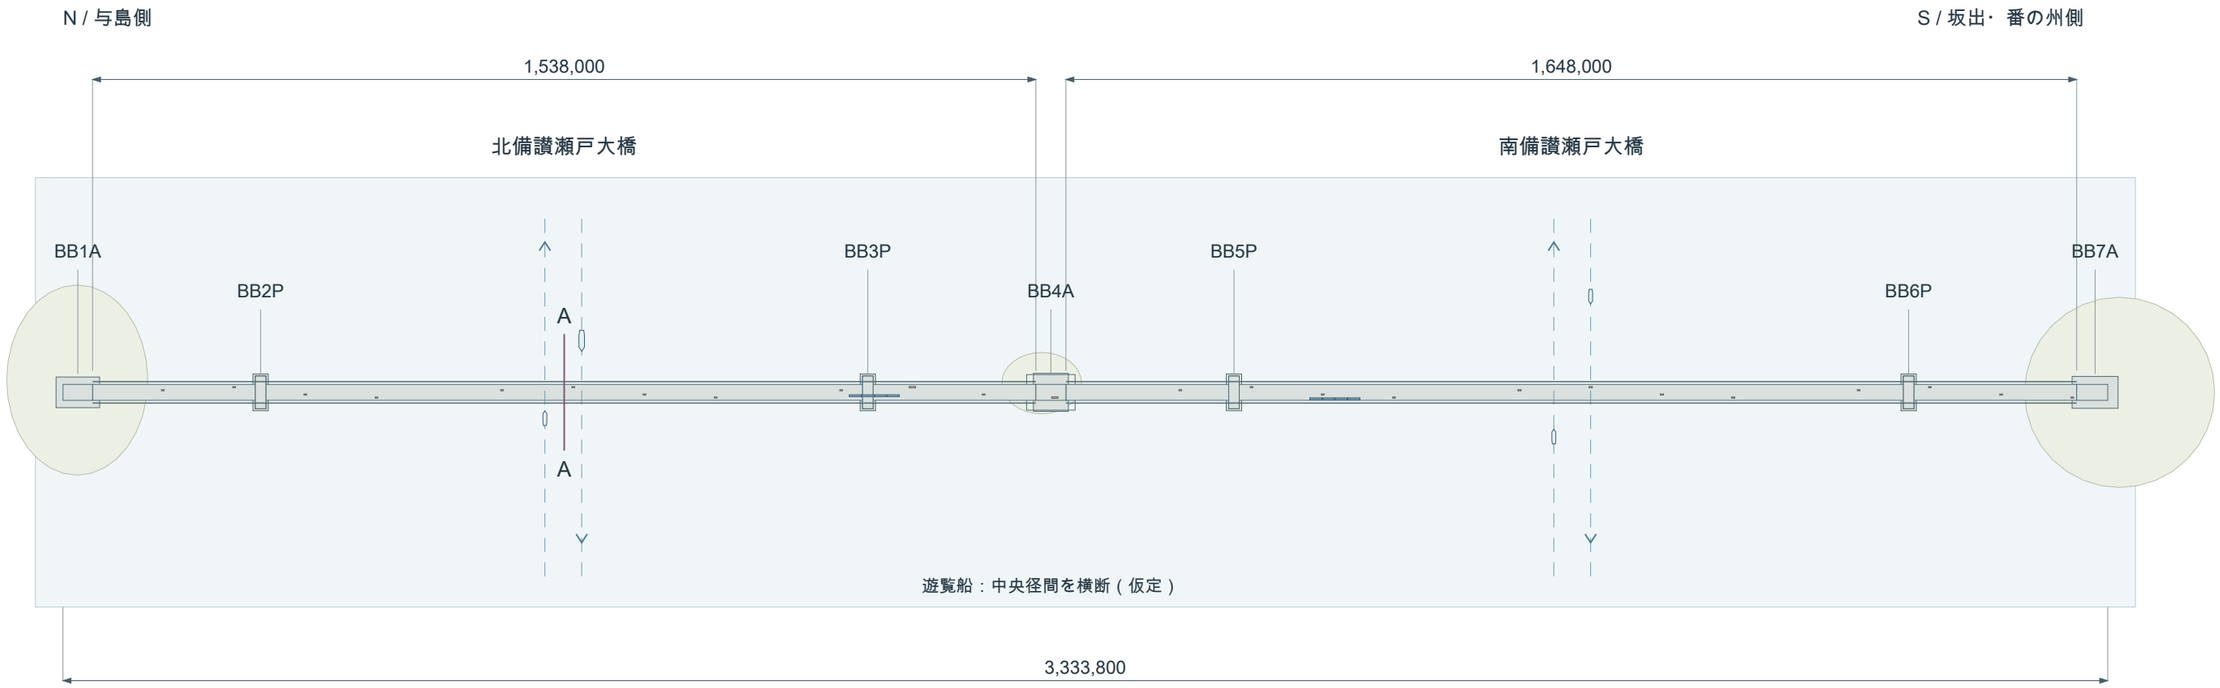

01 対象範囲と公表寸法

北：274,000 + 990,000 + 274,000 = 1,538,000 mm

南：274,000 + 1,100,000 + 274,000 = 1,648,000 mm

BB4Aは一つの共用アンカレイジ。接続区間は49,000 mm。


橋端間3,333,800 mm：公表区間1611+1723 mとの丸め差。

A-A：北橋中央径間。下層電車は4両×2編成を投影表示。


参照：JB本四高速 / 川崎製鉄技報。自動車24台・遊覧船4隻・電車2編成は説明用の配置。

車・船・電車はt=0の静止位置。経路・速度は説明用の仮定。

車両（1:100）

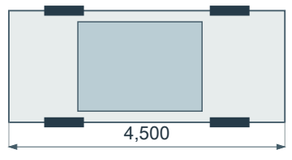


遊覧船（1:500）

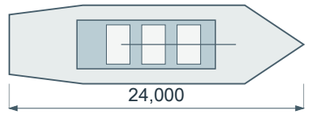

車体・船体・速度・配置は説明用の仮定。Webのみ移動し、CADは静止。

瀬戸大橋 / 南北備讃瀬戸大橋

橋梁全体側面図1:10000（鉛直倍率なし） / 主塔正面1:2000・参考

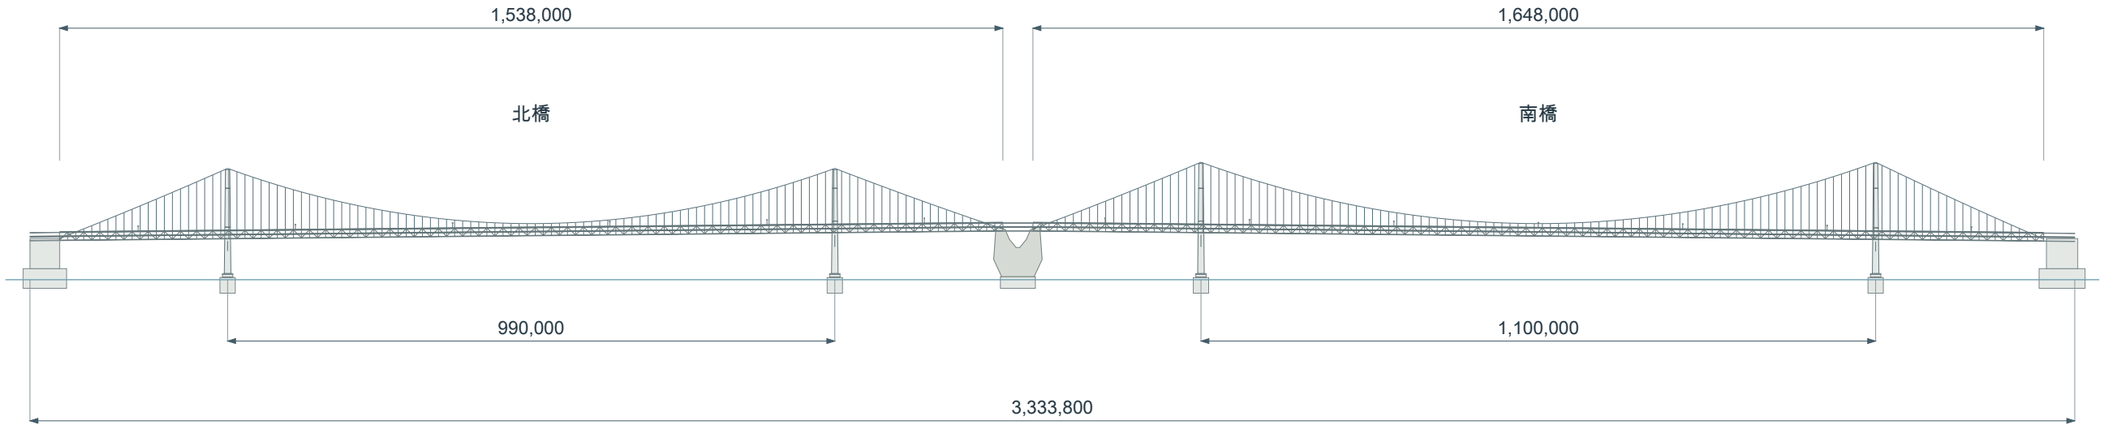

全体側面図：模型の橋面はBB4Aから両側へ約1%低下。北側勾配は南側の対称仮定。


主塔正面図（参考）1:2000

公式の支配寸法


北橋・中央径間	990,000 mm
南橋・中央径間	1,100,000 mm
北橋・主塔頂高	T.P. +184,000 mm
南橋・主塔頂高	T.P. +194,000 mm
北橋・主ケーブル径	998 mm（被覆を除く）
南橋・主ケーブル径	1,062 mm（被覆を除く）

出典：JB本四高速・本四公団 / 塔正面：建設の機械化1986.5 Fig.3・駒井1986 Fig.1。

北橋・3P型

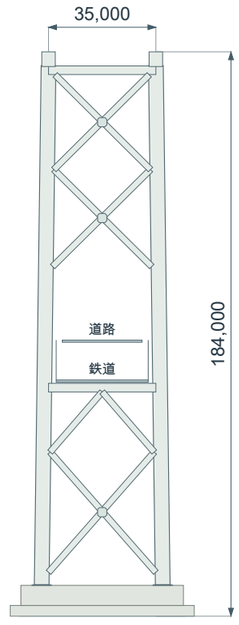


南橋・5P型

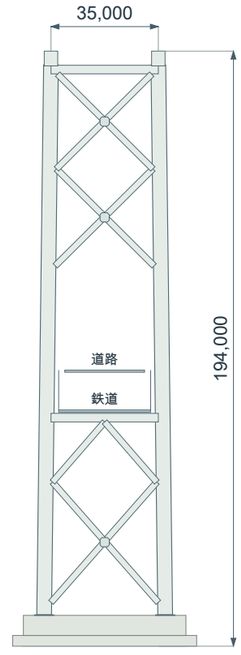


上部2X / 下部X + 山形。塔柱は十字形3セル外包の近似。

瀬戸大橋 / 南北備讃瀬戸大橋

A-A 横断面 1:250 / BB4A通過部 1:750 / 軌頂詳細 1:20

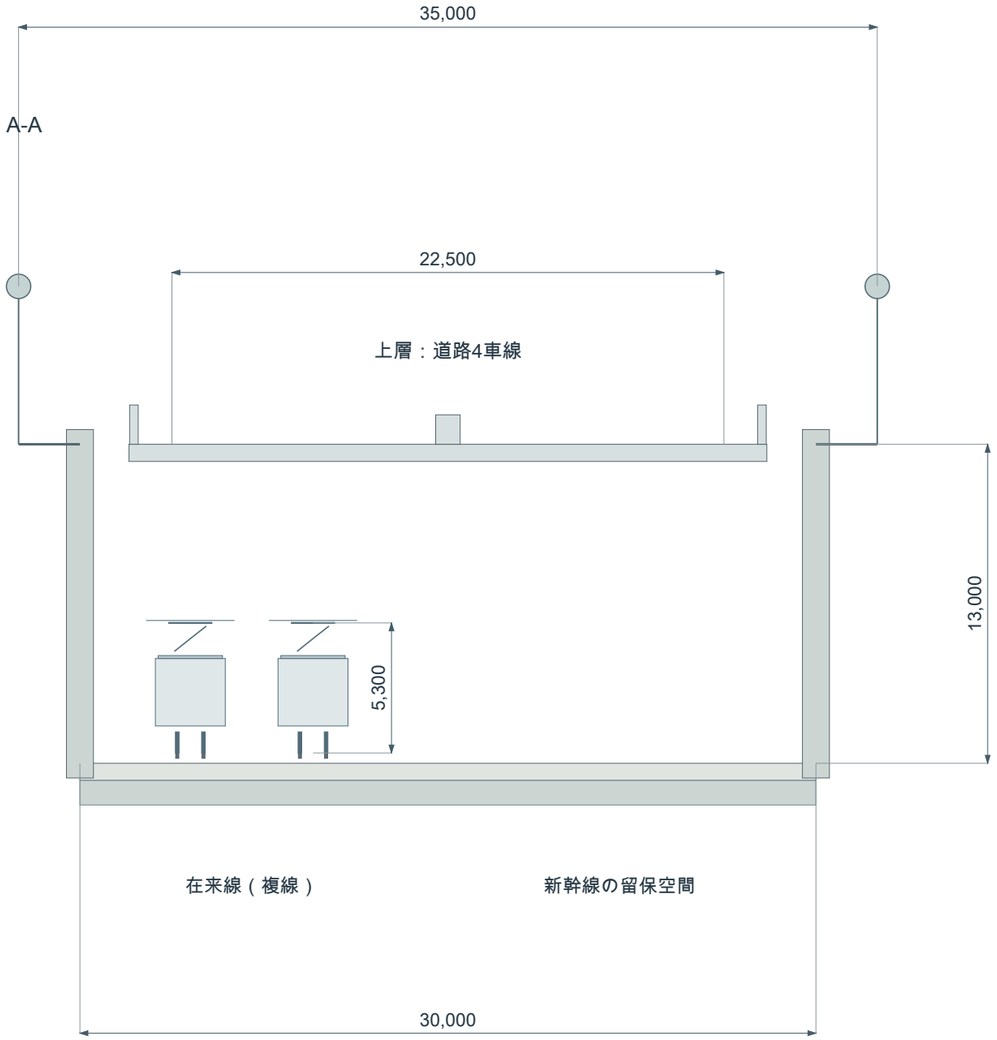


BB4A外形 1:2000

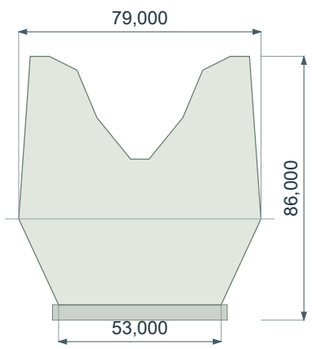


BB4A：下層鉄道の通過断面

通行有効高さ 11,880 mm（仮定）

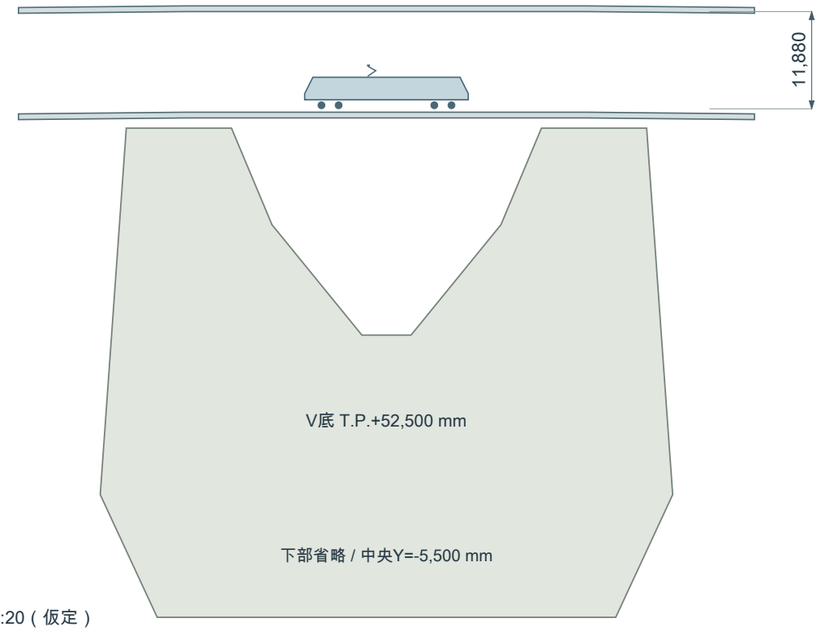

軌頂詳細 1:20（仮定）

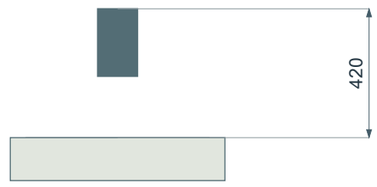

断面 X=-793,500 mm / 北橋中央径間

上層 T.P.+85,065 / 下層 T.P.+72,065 mm（近似）

車両高5,300・架線高5,400 mmは軌頂からの仮定。

横桁を1,200 mm下げ、車輪との干渉を解消。

公表値：主桁間30m・桁高13m・ケーブル間35m。

車両限界・動揺・電気離隔の法定照査は未実施。

寸法はレール頂と下層床上面との差。

開口は説明用の仮定。

原図のアンカレイジを

再現する施工図ではない。

実際の経路・地盤・安全性を保証する断面図ではない。