


木造軸組 候補構造図 / R19


単位 mm / A3 / 確認済み平面を保持 / 演示方案・構造計算未実施 / 2026-10-07

01 1階 柱・梁・耐力壁候補 / 1:50

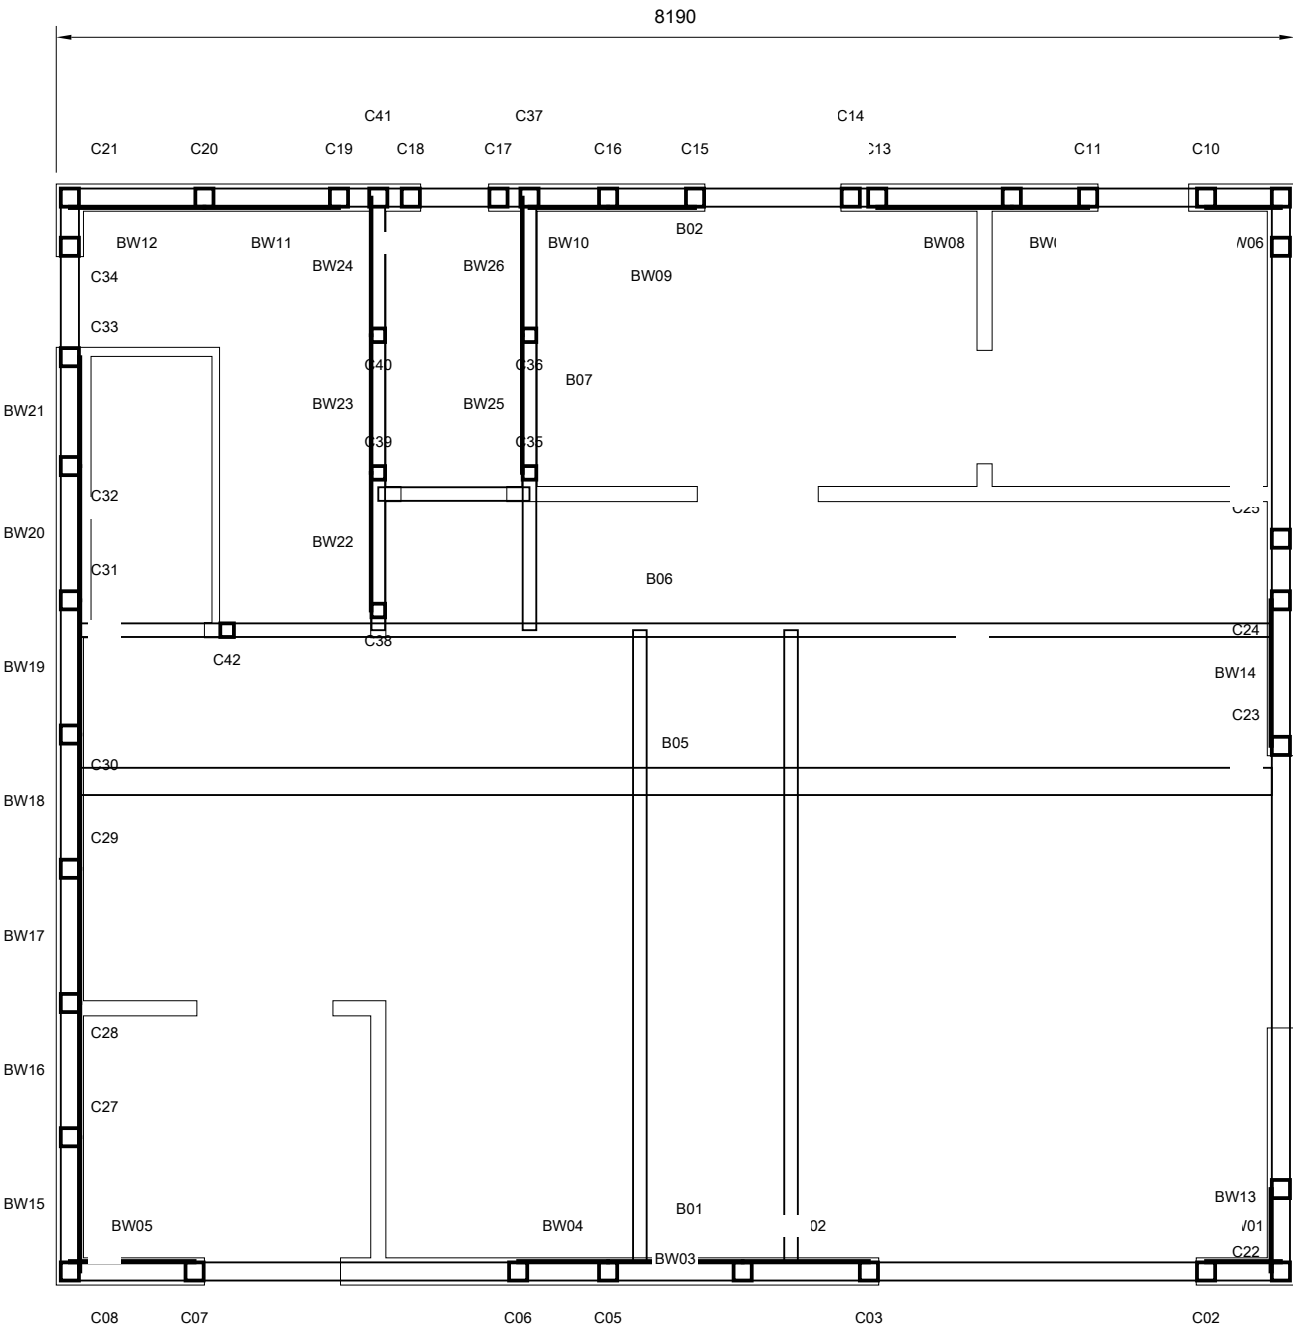

柱: 外周120角 / 内部90角 / 梁: 120・ 90・ 180 × H300
断面寸法はデモ入力。材種・等級・壁倍率・接合耐力は未設定。

02 2階 柱・梁・耐力壁候補 / 1:50

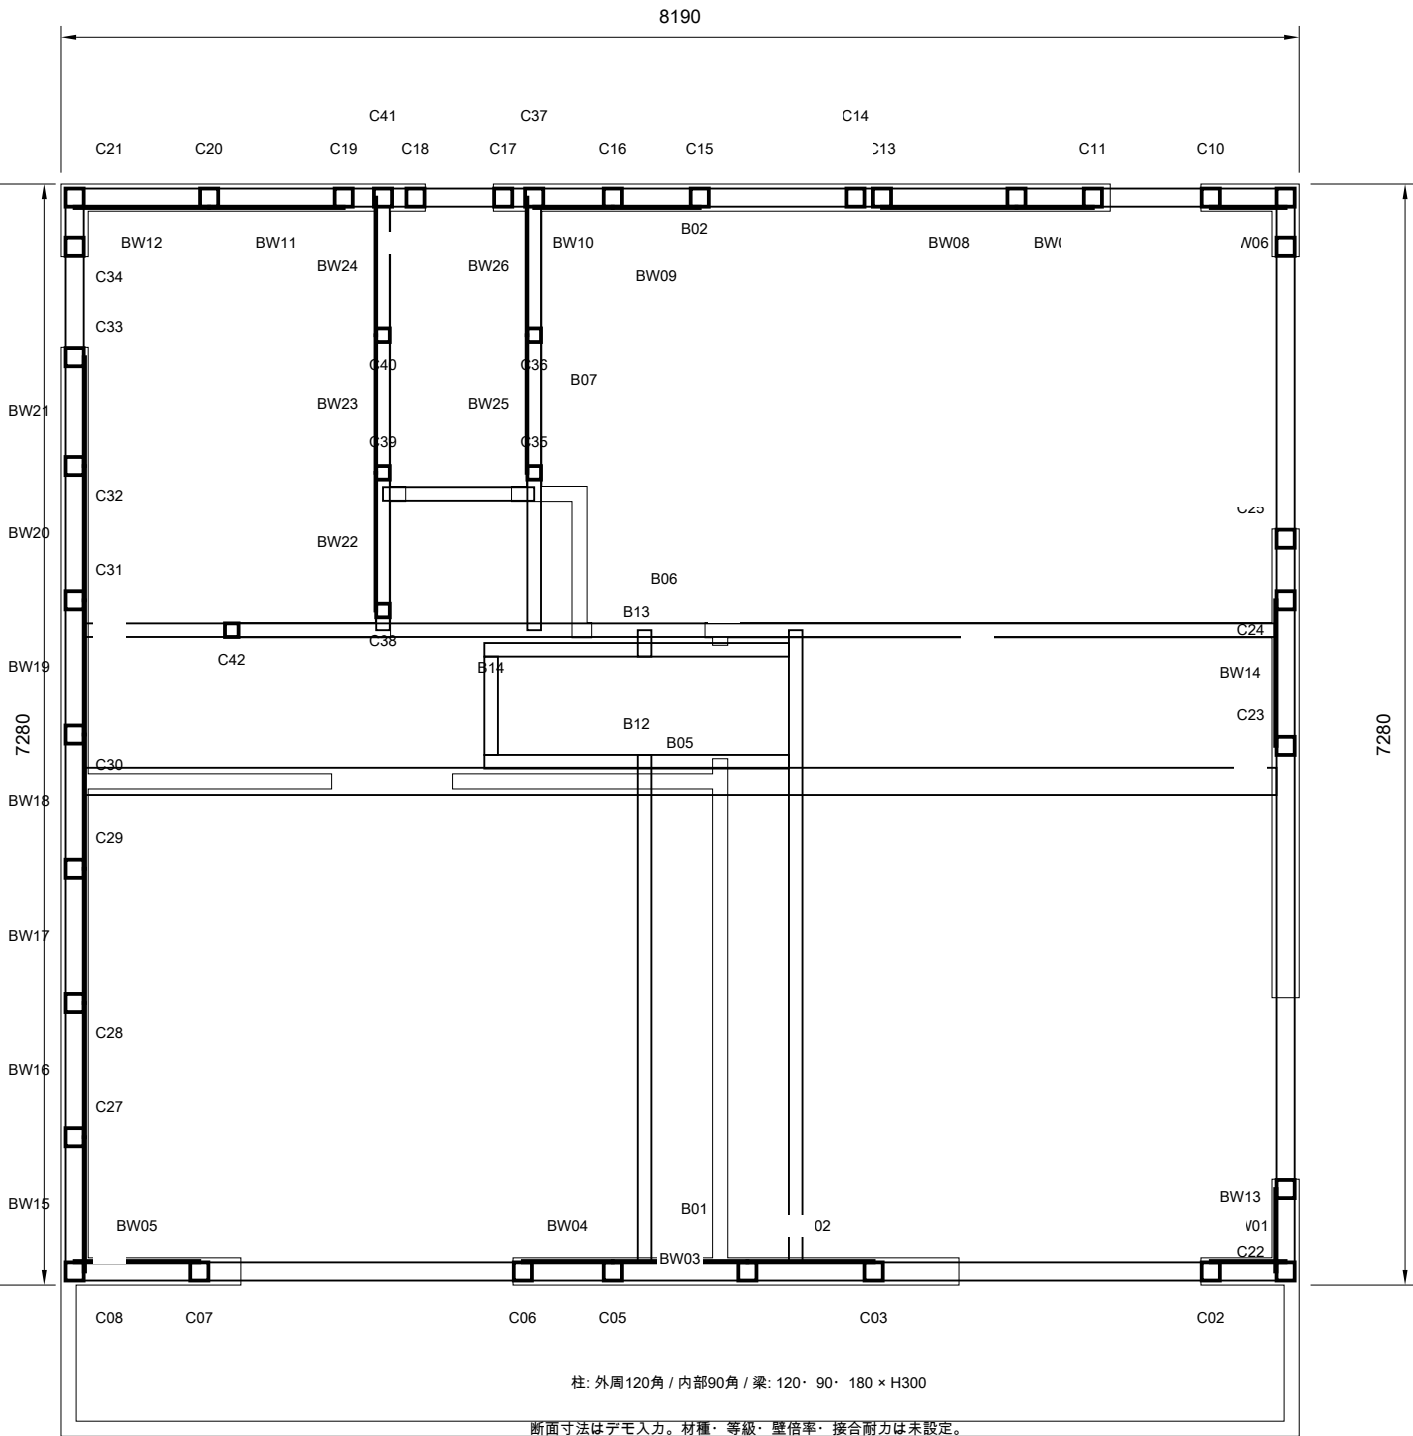

柱: 外周120角 / 内部90角 / 梁: 120・ 90・ 180 × H300
断面寸法はデモ入力。材種・等級・壁倍率・接合耐力は未設定。

C : 柱 / B : 梁 / BW : 耐力壁候補 (倍率未設定) 。必要壁量・偏心・耐震等級を示さない。


B05 : LDK上部の長スパン梁候補。2階壁荷重・たわみ・接合部を含め再設計が必要。

柱位置は両階の閉じた壁内。検修口下はB12～B14で幾何調整。部材・接合耐力は未計算。

基礎支持線・ 小屋裏床組 候補図 / R19


単位 mm / A3 / 平面・ 断面1:75 / 基礎参考断面のみ1:25 / 全寸法はデモ入力

01 基礎支持線候補 / 1:75

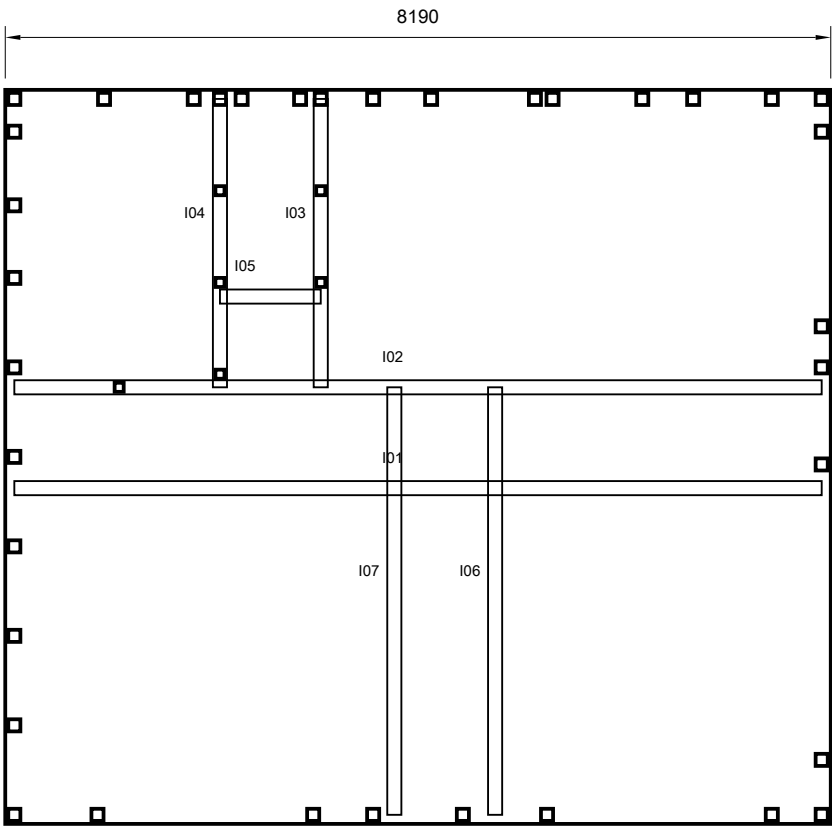


I01～I07：内側支持肋 / 幅140 / 上端Z=-200 (仮定)
地盤・ 反力・ 配筋・ 沈下を計算して断面を決める。

02 小屋裏床組・ 検修口 / 1:75

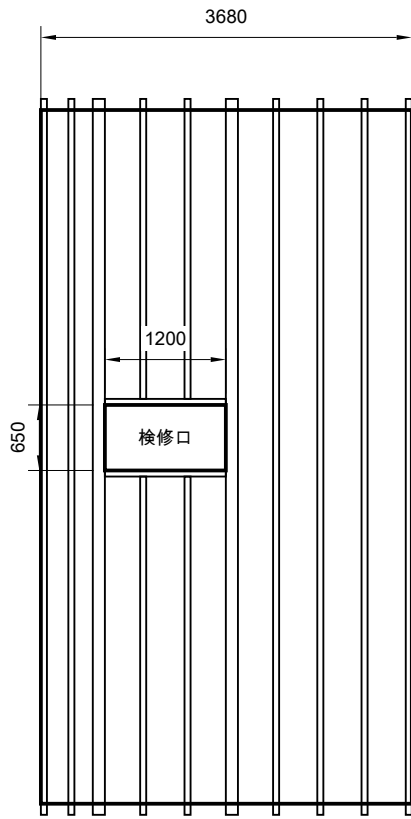


根太60×H180・ 間隔≤455 / 開口両側120幅
開口補強梁60×H180 / 全て断面未計算

03 東西参考断面 / 1:75 (Zは実座標)

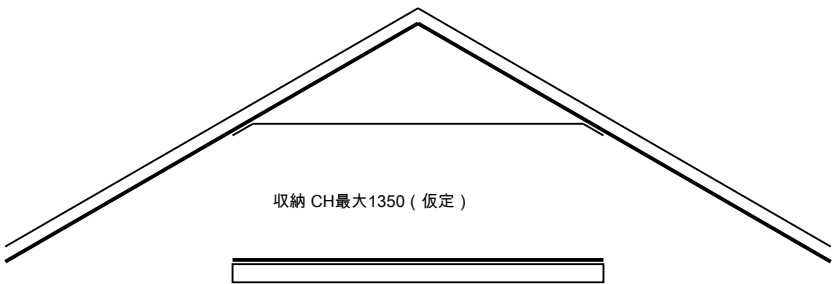

屋根材内部の表示用材寸法は未計算。屋根構成・ 梁せいを再設計。

04 基礎参考断面 / 1:25

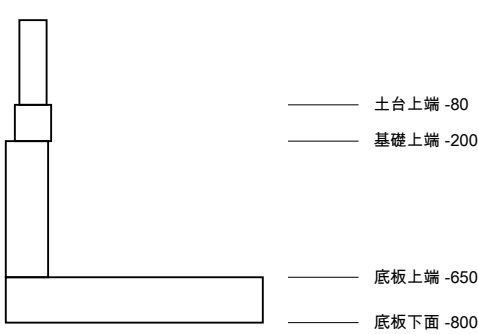

底板150・ 立上り140・ 土台120：デモ入力

支持肋は外周と交差部を整理。接触は耐力の証明ではない。

所在地・ 地盤・ 材料等級・ 積載荷重は未指定。engineering_inputs_R06.jsonの未設定項目を要入力。

耐力壁量・ 偏心・ 梁の曲げ / セン断 / たわみ・ 接合部・ 基礎支持力・ 配筋・ 沈下は未計算。

収納の不算入・ 用途・ 天井処理は所在地で要確認。図面は構造計算書・ 確認申請・ 施工図ではない。