


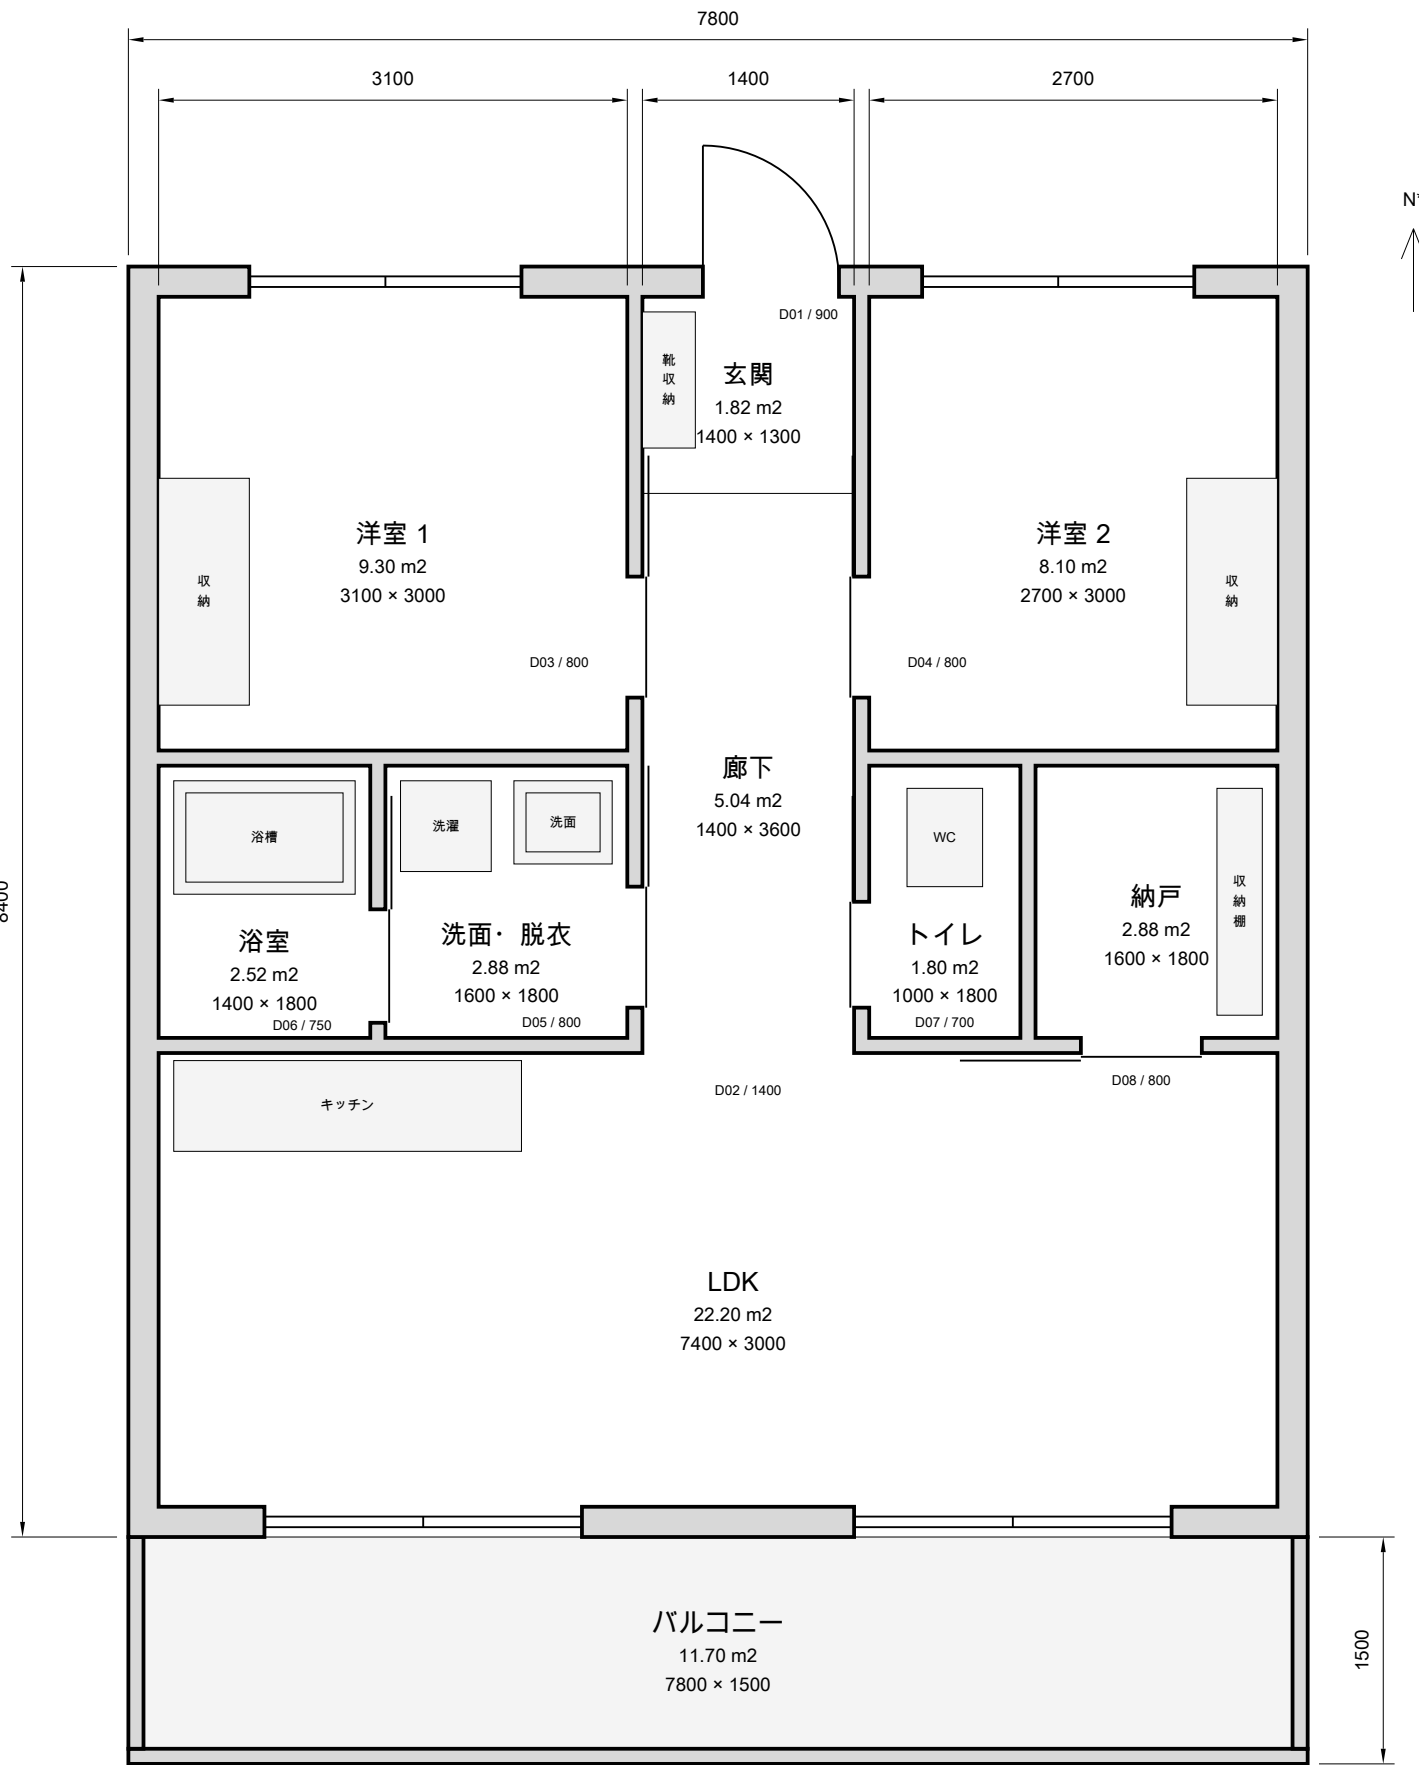

## 2LDK / 平面図 / A01

寸法単位 mm / 全寸法・方位は仮定

## 日本の集合住宅 / 2LDK

### 単一住戸の参考計画

#### 面積の区分 / AREA DEFINITIONS

外輪郭面積 65.52 m2 (7800 × 8400)

室内正味面積 56.54 m2 (壁を除く各室合計)

バルコニー 11.70 m2 (別計上・板面投影)

室内面積は収納・設備の占有部分を含む。

登記面積・専有面積・法定床面積ではない。

#### 計画条件 / DEMONSTRATION ASSUMPTIONS

全寸法・北向・北側共用廊下・南側バルコニーは仮定。

階高2800 / 室内有効高さ2500 / 床スラブ200。

外壁・戸境壁200 / 間仕切100 / 廊下幅1400。

玄関の靴収納350を除いた通路は1050。

浴室1400 × 1800 / 洗面脱衣1600 × 1800。

洋室の北窓は腰高1100、LDK南面は掃き出し窓。

北側出入口は外開き。共用廊下の寸法は未検討。

移動経路: 玄関 → 廊下 → 両洋室・洗面・便所・LDK。

LDK → 納戸・バルコニー / 洗面脱衣 → 浴室。

#### 建具 / OPENINGS (rough widths in mm)

D01 玄関900 / D02 LDK開口1400

D03 洋室1 800 / D04 洋室2 800

D05 洗面800 / D06 浴室750 / D07 便所700

D08 納戸800: LDK側の外付けレールで西へ引く。

室内引戸は外付け概念。3Dの戸は閉位置で表示。

#### 図面情報 / DRAWING INFORMATION

A3 横 420 × 297 / 縮尺1:50 / 単位mm / A01

令和8年10月5日 / text-to-cad + ezdxf

東京都建設局 CAD製図基準 令和6年4月: 共通規定準用。

土木基準の住宅への参考適用。SXF電子納品ではない。

構造・設備・採光換気・消防・法規適合は未検証。

家具・建具・バルコニー手すりは概念形状。