
東京タワー / 基座平面図

LANDMARK-R04 | A3 | 1:500 | 単位 mm | 外観模式図

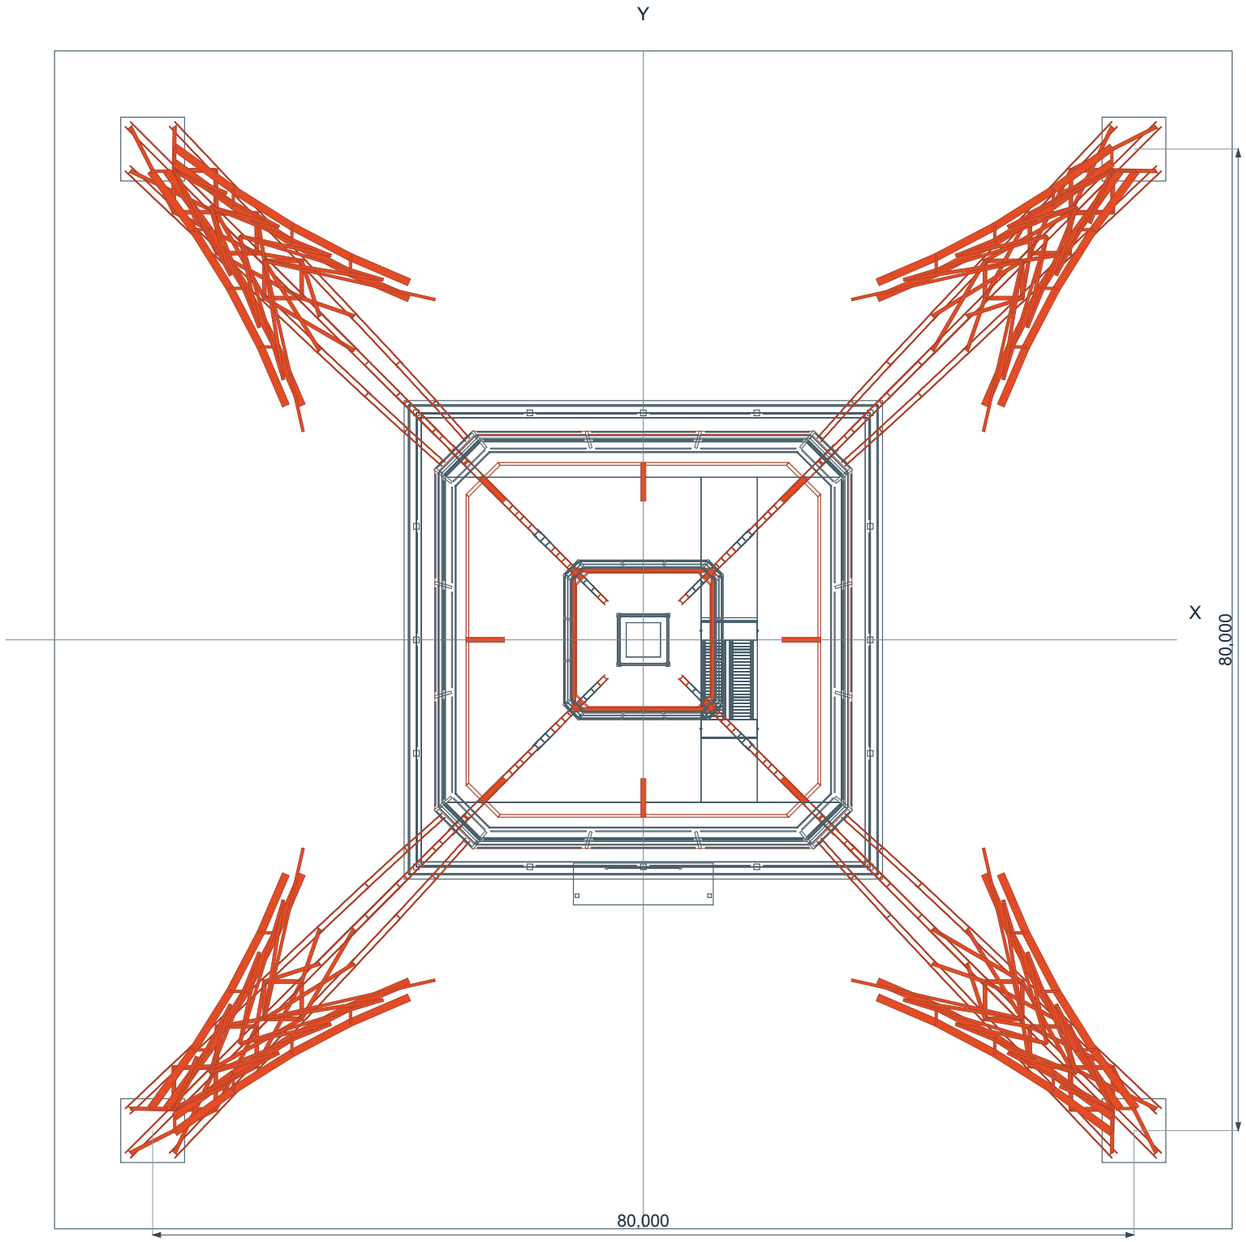

基座・足元 / 上部の投影外形を重ねた模式配置

方位はモデル軸のみ。実際の敷地方位・配置とは異なります。

公表値を参照 / 未測量・未計算 / NOT FOR CONSTRUCTION

モデル寸法と図面の対応

01 公式案内の公表値

全高 333,000 mm

メインデッキ150 m / トップデッキ250 m

02 モデル座標・参照資料

施工GLの構架帯を参考に外殻を配置。

下層120,000 / 上層125,000 mm（解釈）

上部外殻参照223,550 mm（H23帯）

H11/H23からの床同定・層間は仮定。

公式案内値との換算・完成面実測ではない。

塔脚基準軸線間80,000 mmは図1参照。

部材断面・接合・平面外形は仮定。

03 座標とデータ

CADモデル空間は実寸1:1、単位mm。

平面はX/Y、立面はX/Zの正投影。

方位はモデル用。測量方位は未設定。

基座平面は上部投影外形も重ねて表示。

文字・寸法はDXFで編集可能。

04 参照資料（2026-10-30）

宮地技報 No18 p86 図1（2002年改修）


tokyotower.co.jp/guidance/

観光床の完成面・現況構造は未測量。

text-CAD | LANDMARK-R04 | 2026-10-30

東京タワー / 正立面図

LANDMARK-R04 | A3 | 1:1500 | 単位 mm | 外観模式図

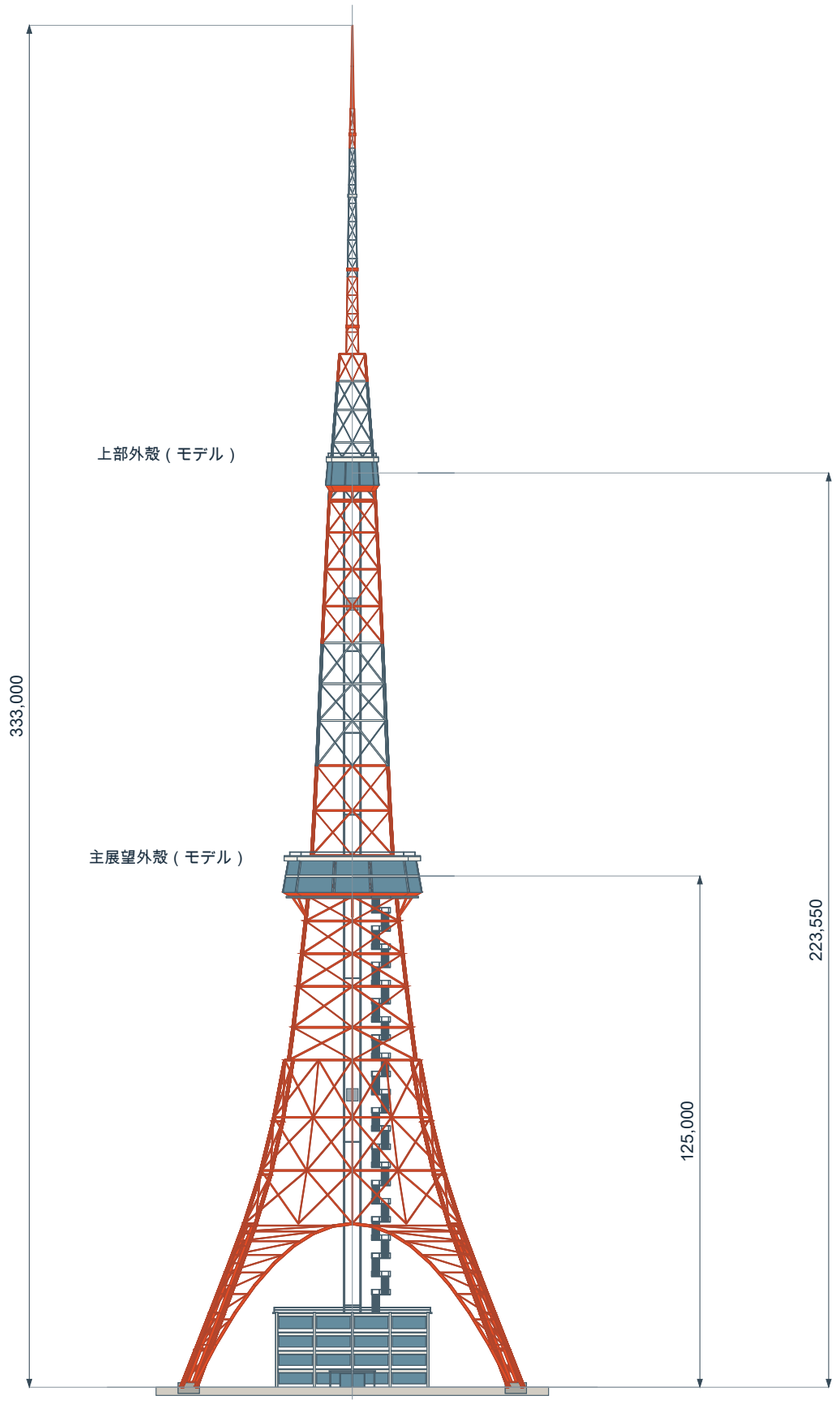

基準 GL ±0

正投影 / 展望施設の形状・鉄骨径は模式表現

公表値を参照 / 未測量・未計算 / NOT FOR CONSTRUCTION

モデル寸法と図面の対応

01 公表値とモデル座標

公式案内: メイン150 m / トップ250 m

全高 333,000 mm / 公表値

施工GLの構架帯に関連付けた解釈的配置:

モデル下層120,000 / 上層125,000 mm


上部外殻参照223,550 mm（H23帯）

床との対応・5,000 mm層間はモデル仮定。

公式案内値との換算・完成面実測ではない。

部材断面・接合・外形は独自の仮定。

02 メインデッキ付近 / 1:300

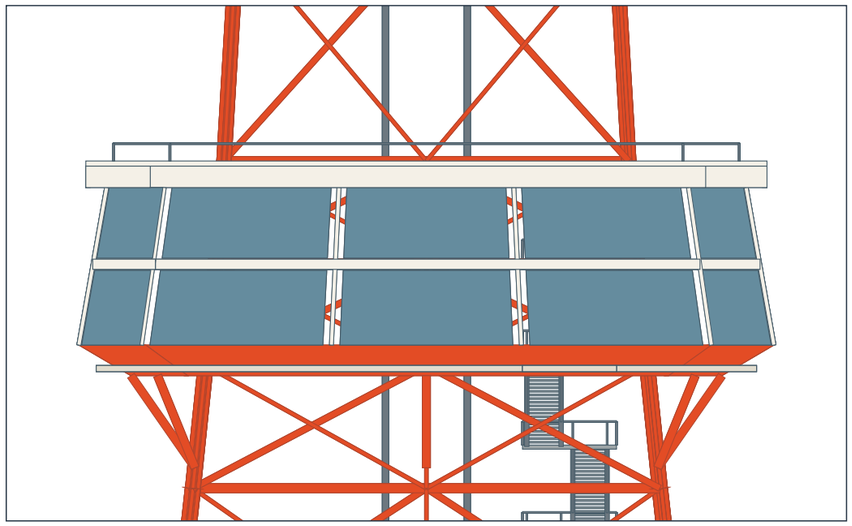

宮地技報 No18 p86 図1 / 施工GL参照

公式案内の150/250 mを変更するものではない。

CAD mm / X-Z正投影 / 編集可能な文字・寸法

未測量・未計算 / tokyotower.co.jp/guidance/


text-CAD | LANDMARK-R04 | 2026-10-30

東京タワー / 鋼接合部・節点詳細


LANDMARK-R04 | A3 | モデル空間 1:1 | 単位 mm | 外観模式図

公表値: 全高333,000 mm・公式案内150/250 m / モデル外殻125/223.55 mは解釈配置（完成面未測量）。

節点位置 / 下部〜主展望台 / 1:1000

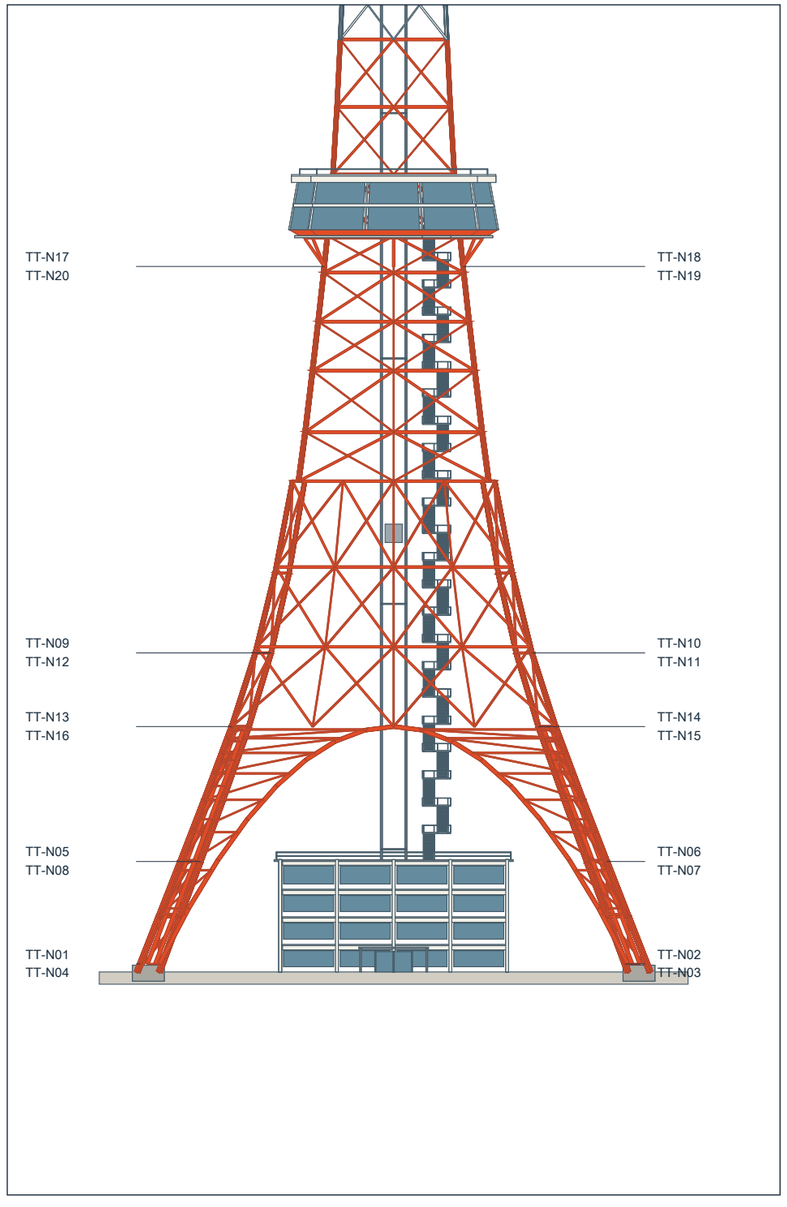


TT-N01 塔脚板組 1 / 1:20

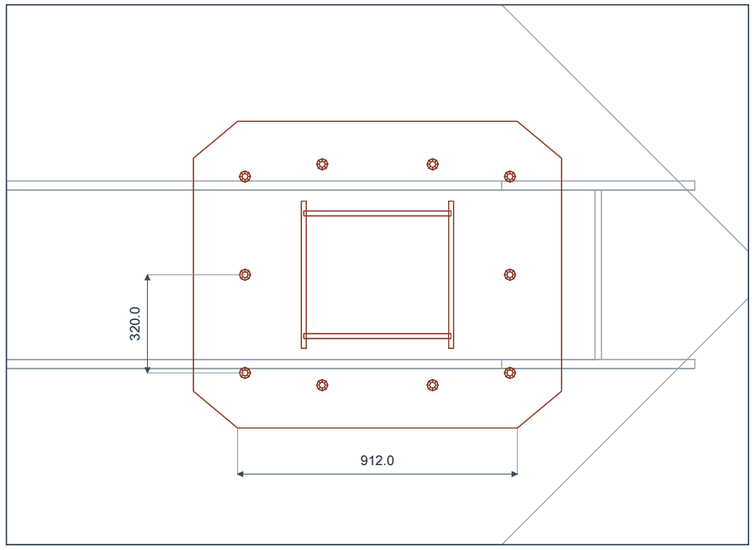

板厚 t=30 mm / 板幅・心々寸法 mm / 全て仮定

TT-N05 下部集合節点 1 / 1:20

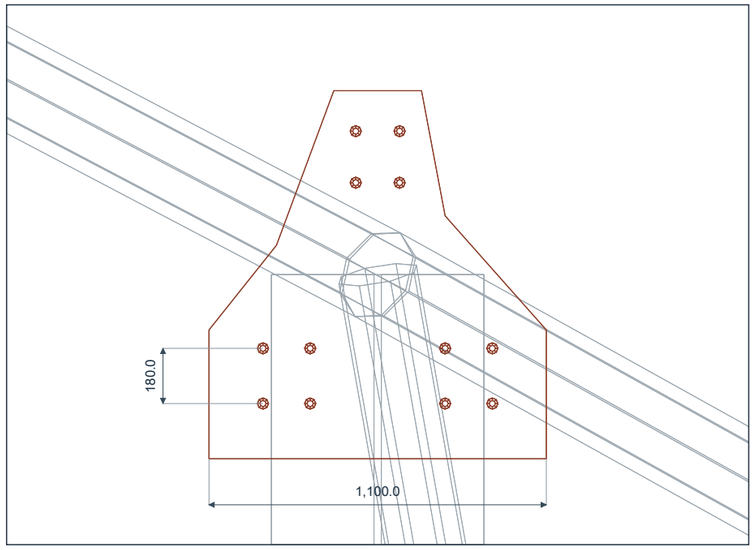


板厚 t=20 mm / 板幅・心々寸法 mm / 全て仮定

TT-N13 主材両面継手 1 / 1:20



板厚 t=16 mm / 板幅・心々寸法 mm / 全て仮定

TT-N17 主展望台支持節点 1 / 1:20

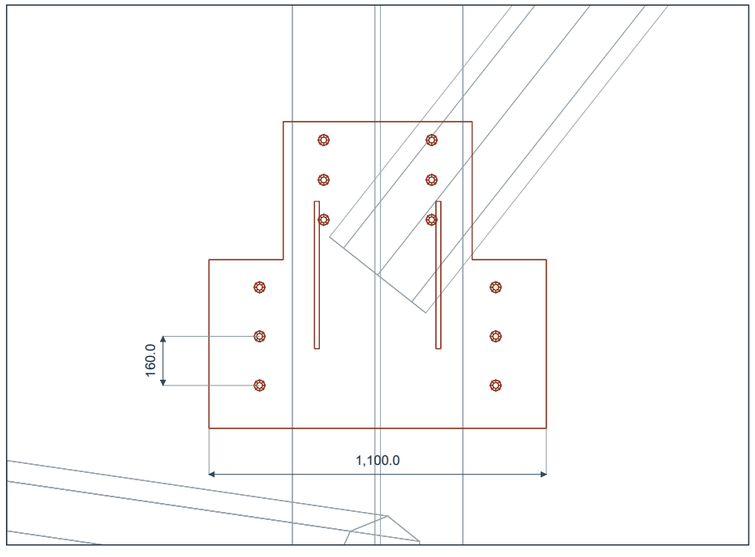

板厚 t=24 mm / 板幅・心々寸法 mm / 全て仮定

板面の正投影。板厚は注記、板幅とリベット心々は実寸の編集可能な寸法。

未測量・未計算 / NOT FOR CONSTRUCTION / 原建物の接合詳細ではありません。