


1階平面図

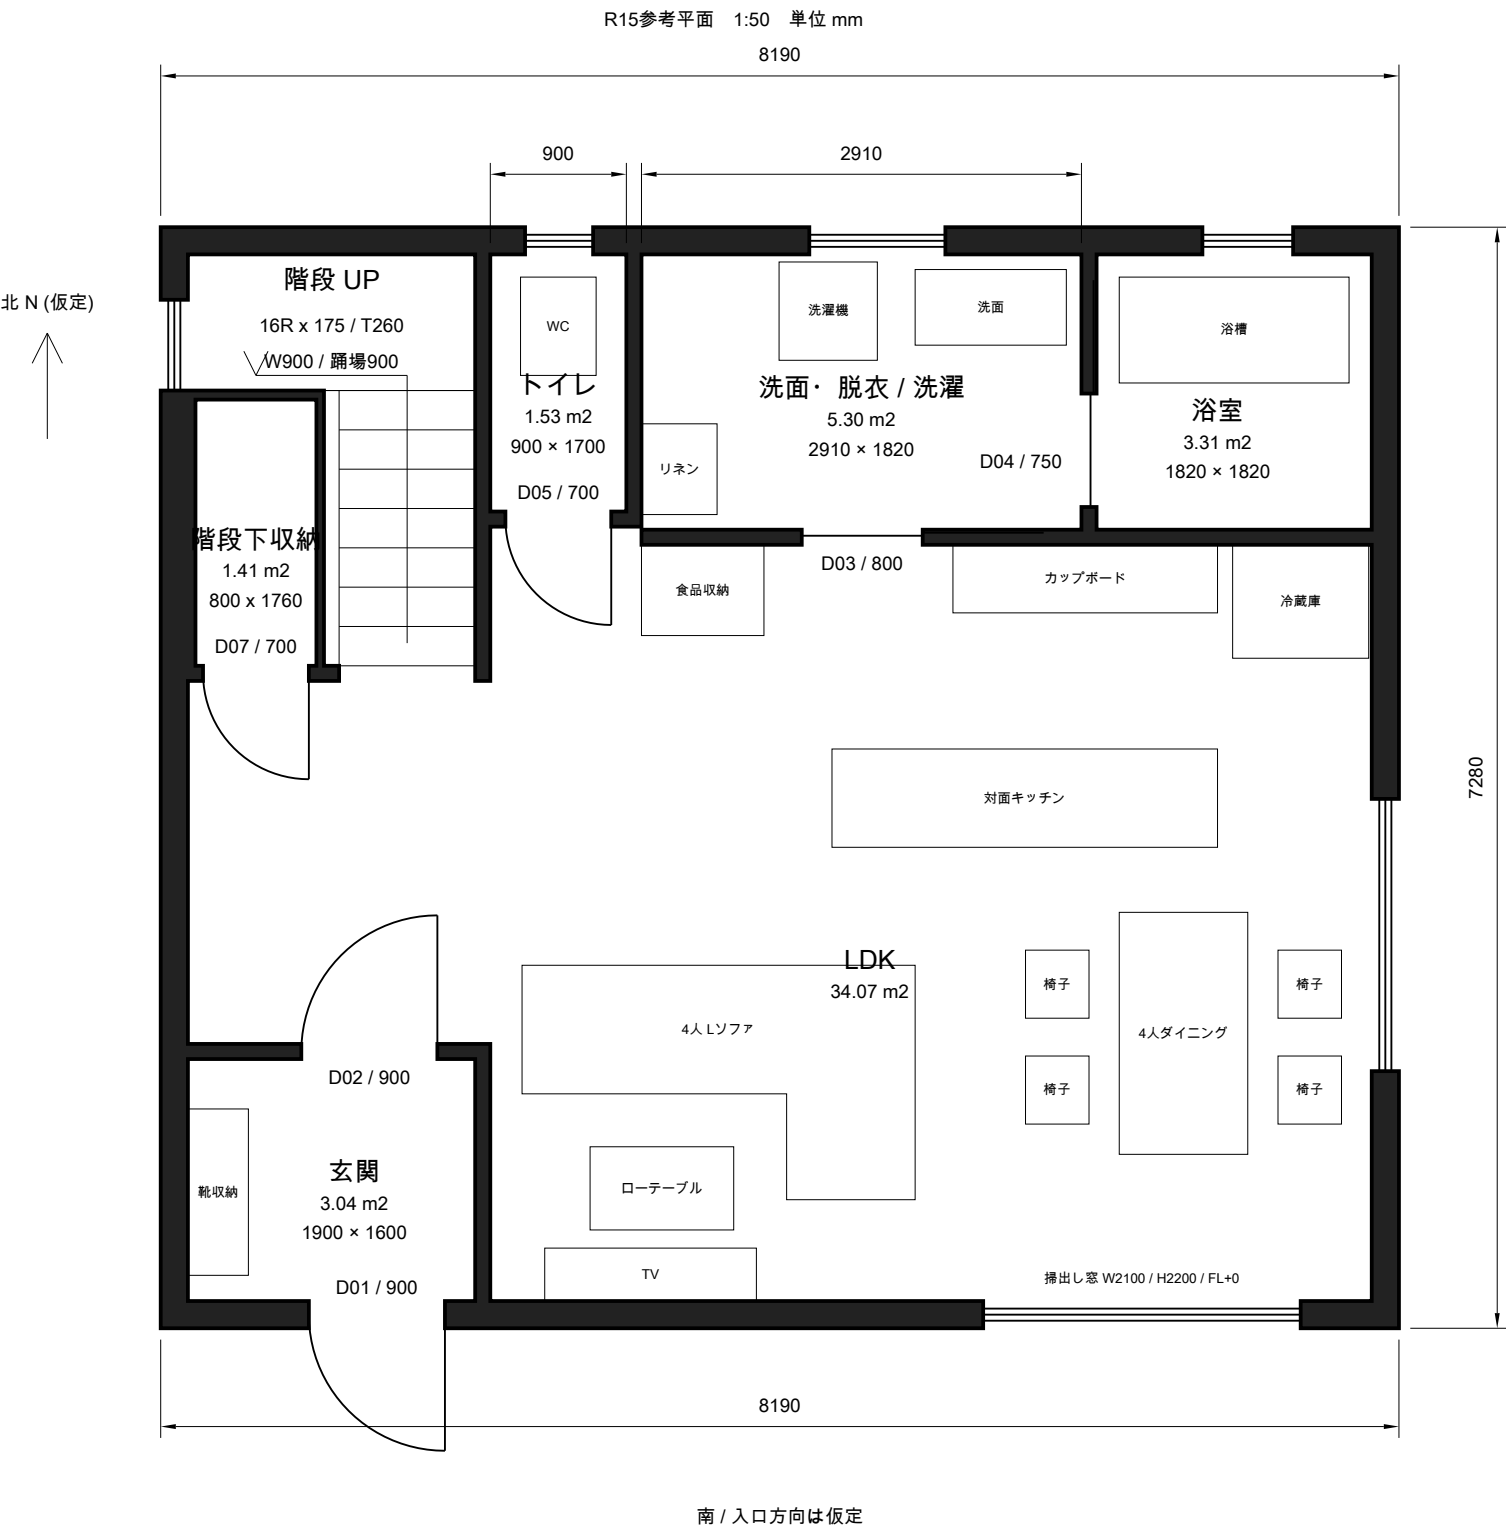

室別面積表 (内法)

室名	面積 (m²)
LDK	34.07
玄関	3.04
浴室	3.31
洗面・脱衣 / 洗濯	5.30
トイレ	1.53
階段 (階段室)	3.53
階段下収納	1.41

注意事項・仮定条件

01. 建物外形 8,190×7,280、階高 2,800 mm はデモ用の仮定寸法。
02. 外壁 180、内壁 100 mm。家具・建具の寸法は計画上の仮定。
03. R15階段下収納・4人家具。南西玄関・北西階段、西側は階段窓のみ。
04. 面積は壁内法の概算で家具占有分を含む。建築確認申請の面積ではない。
05. 廊下面積は階段を除く。階段面積は階段室の確保範囲を示す。
06. 階段：16R×175、T260、階段幅 900、踊場 900 mm。
07. 対面キッチン2550×650・背面通路900。小屋裏北側換気窓600×300は仮定。
08. 南側LDK・2寝室は掃出し窓H2200/FL+0。ガラス・建具・防水・耐力は未設計。
09. 便所：内法 900×1,700 mm。出入口 700 mm は枠厚を控除する前の寸法。
10. 構造・防火・耐震・法令適合は未検証。施工図として使用不可。
11. 東京都土木CAD製図基準 (令和6年4月) を住宅の図式に準用。
12. 南側バルコニー8190×1000は仮定。柱なし・ポーチ先端300露出。耐力・防水・排水は未設計。

凡例

実線：壁・建具・家具の平面輪郭


寸法線：壁内法・建物外形・建具開口幅

D01 等：建具番号 UP：上り方向

北矢印：仮定方位 R15：左右反転・対面キッチン・北側換気窓・構造未計算

施設名	住宅参考	
工事件名	日本一戸建て計画	
工事箇所	未定	
図面名称	1階平面図	
縮尺	1:50	図面番号
作製年月日	令和8年10月7日	001
事業所名 未定		全2枚

2階平面図

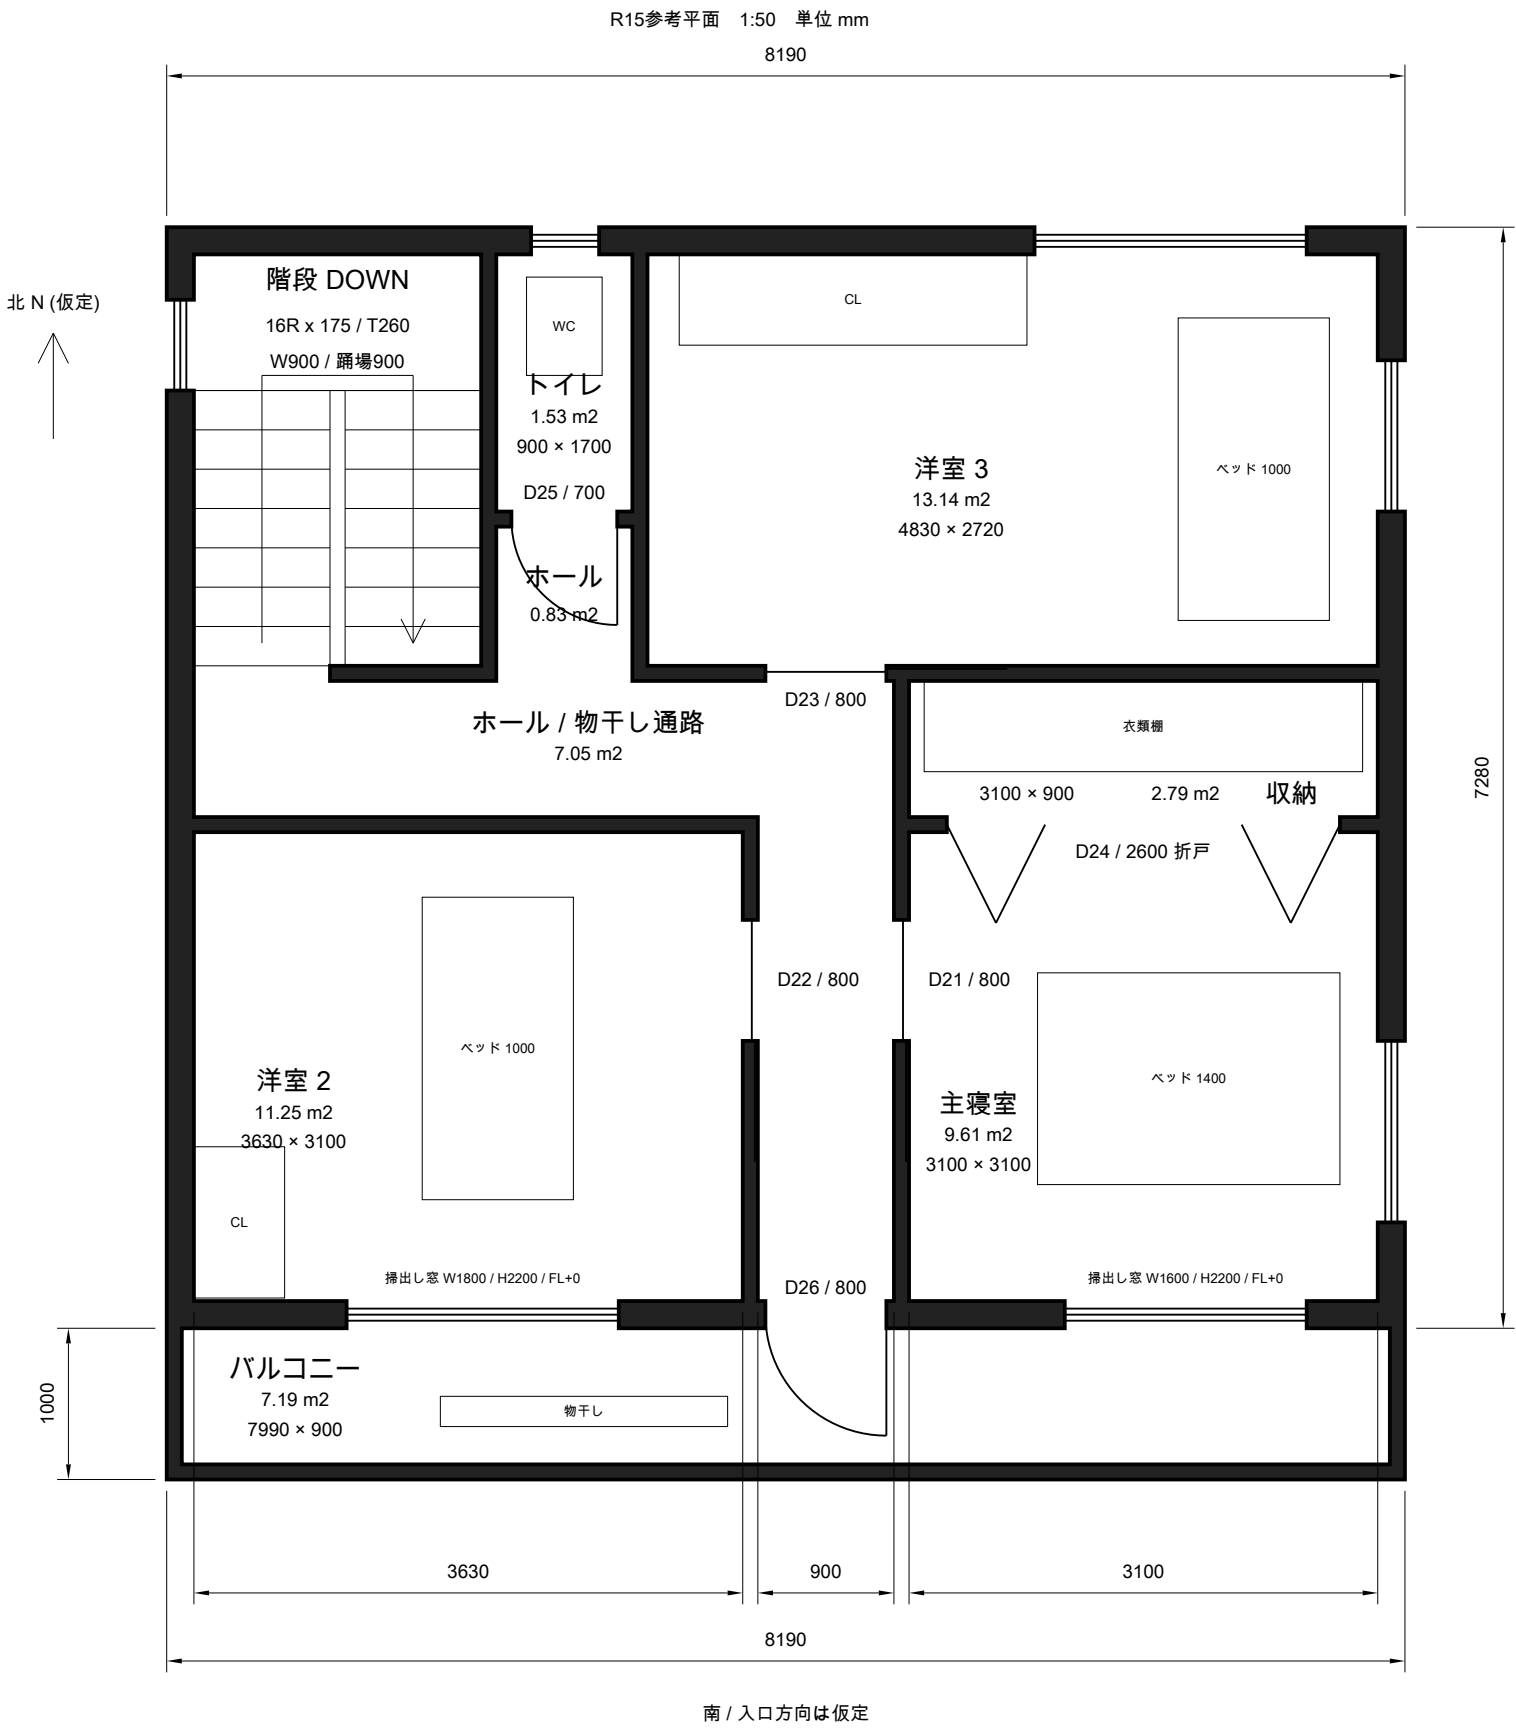

室別面積表 (内法)

室名	面積 (m ²)
主寝室	9.61
収納	2.79
洋室 2	11.25
洋室 3	13.14
ホール / 物干し通路	7.05
トイレ	1.53
ホール	0.83
階段 (階段室)	5.17
バルコニー	7.19

注意事項・仮定条件

01. 建物外形 8,190×7,280、階高 2,800 mm はデモ用の仮定寸法。
02. 外壁 180、内壁 100 mm。家具・建具の寸法は計画上の仮定。
03. R15階段下収納・4人家具。南西玄関・北西階段、西側は階段窓のみ。
04. 面積は壁内法の概算で家具占有分を含む。建築確認申請の面積ではない。
05. 廊下面積は階段を除く。階段面積は階段室の確保範囲を示す。
06. 階段：16R×175、T260、階段幅 900、踊場 900 mm。
07. 対面キッチン2550×650・背面通路900。小屋裏北側換気窓600×300は仮定。
08. 南側LDK・2寝室は掃出し窓H2200/FL+0。ガラス・建具・防水・耐力は未設計。
09. 便所：内法 900×1,700 mm。出入口 700 mm は枠厚を控除する前の寸法。
10. 構造・防火・耐震・法令適合は未検証。施工図として使用不可。
11. 東京都土木CAD製図基準 (令和6年4月) を住宅の図式に準用。
12. 南側バルコニー8190×1000は仮定。柱なし・ポーチ先端300露出。耐力・防水・排水は未設計。

凡例

実線：壁・建具・家具の平面輪郭

寸法線：壁内法・建物外形・建具開口幅

D01 等：建具番号 UP：上り方向

北矢印：仮定方位 R15：左右反転・対面キッチン・北側換気窓・構造未計算

施設名	住宅参考	
工事件名	日本一戸建て計画	
工事箇所	未定	
図面名称	2階平面図	
縮尺	1:50	図面番号
作製年月日	令和8年10月7日	002
事業所名 未定		全2枚