


1階平面図

尺度 1:50 単位 mm 計画参考図

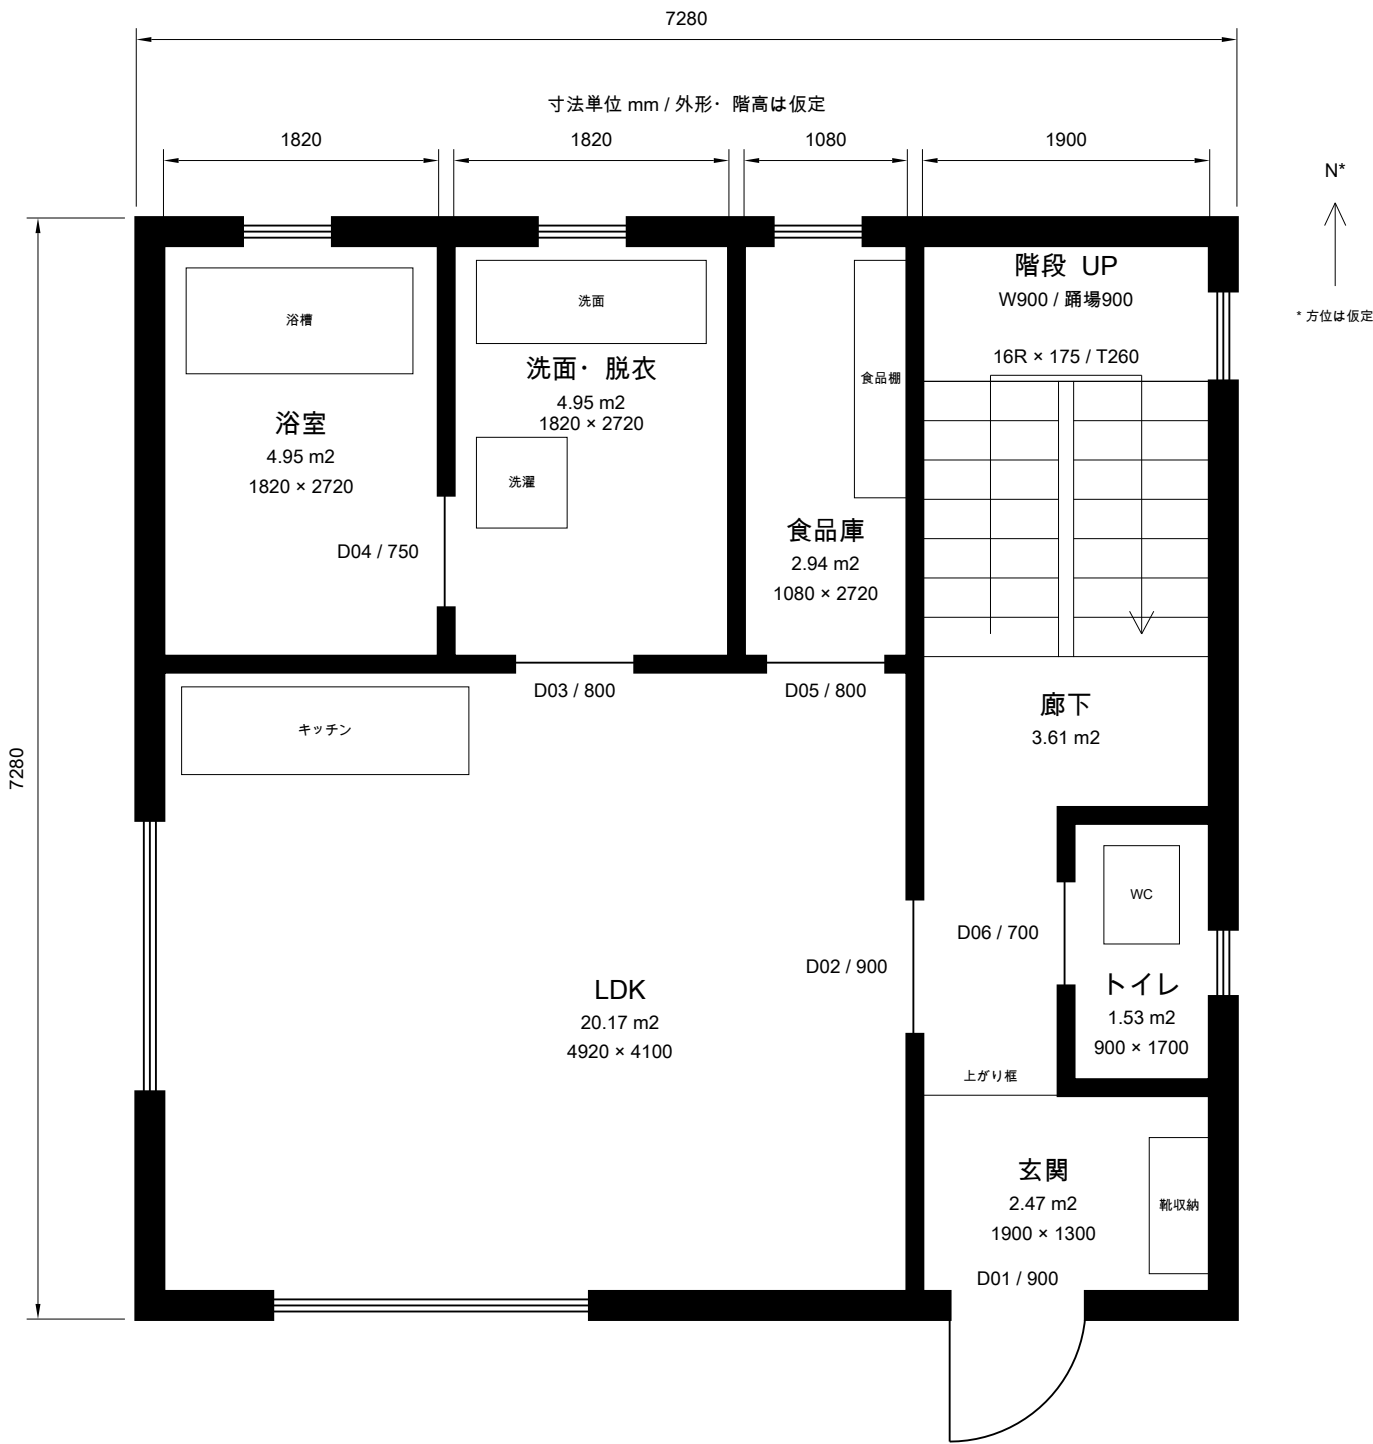

R02 / 1階 平面図 (参考計画)

室別面積表 (内法)

室名	面積 (m ²)
LDK	20.17
浴室	4.95
洗面・脱衣	4.95
食品庫	2.94
玄関	2.47
トイレ	1.53
廊下	3.61
階段 (階段室)	5.17

注意事項・仮定条件

01. 建物外形 7,280×7,280、階高 2,800 mm はデモ用の仮定寸法。
02. 外壁 180、内壁 100 mm。家具・建具の寸法は計画上の仮定。
03. 方位と南側玄関は仮定。敷地・道路・配置条件は未設定。
04. 面積は壁内法の概算で家具占有分を含む。建築確認申請の面積ではない。
05. 廊下面積は階段を除く。階段面積は階段室の確保範囲を示す。
06. 階段：16R×175、T260、階段幅 900、踊場 900 mm。
07. 2階の階段室は床開口。踏板・手すりの詳細は別途設計。
08. 窓・扉は仮配置。引戸の戸袋・枠厚・製品仕様は未設計。
09. 便所：内法 900×1,700 mm。出入口 700 mm は枠厚を控除する前の寸法。
10. 構造・防火・耐震・法令適合は未検証。施工図として使用不可。
11. 東京都土木CAD製図基準 (令和6年4月) を住宅の図式に準用。
12. 既存 A3横・1:50 を継承。SXF電子納品は今回の対象外。

凡例

実線：壁・建具・家具の平面輪郭

寸法線：壁内法・建物外形・建具開口幅


D01 等：建具番号 UP：上り方向

北矢印：仮定方位 R02：製図様式改訂

施設名	住宅参考	
工事件名	日本一戸建て計画	
工事箇所	未定	
図面名称	1階平面図	
縮尺	1:50	図面番号
作製年月日	令和8年10月4日	001
事業所名 未定		全2枚

2階平面図

尺度 1:50 単位 mm 計画参考図

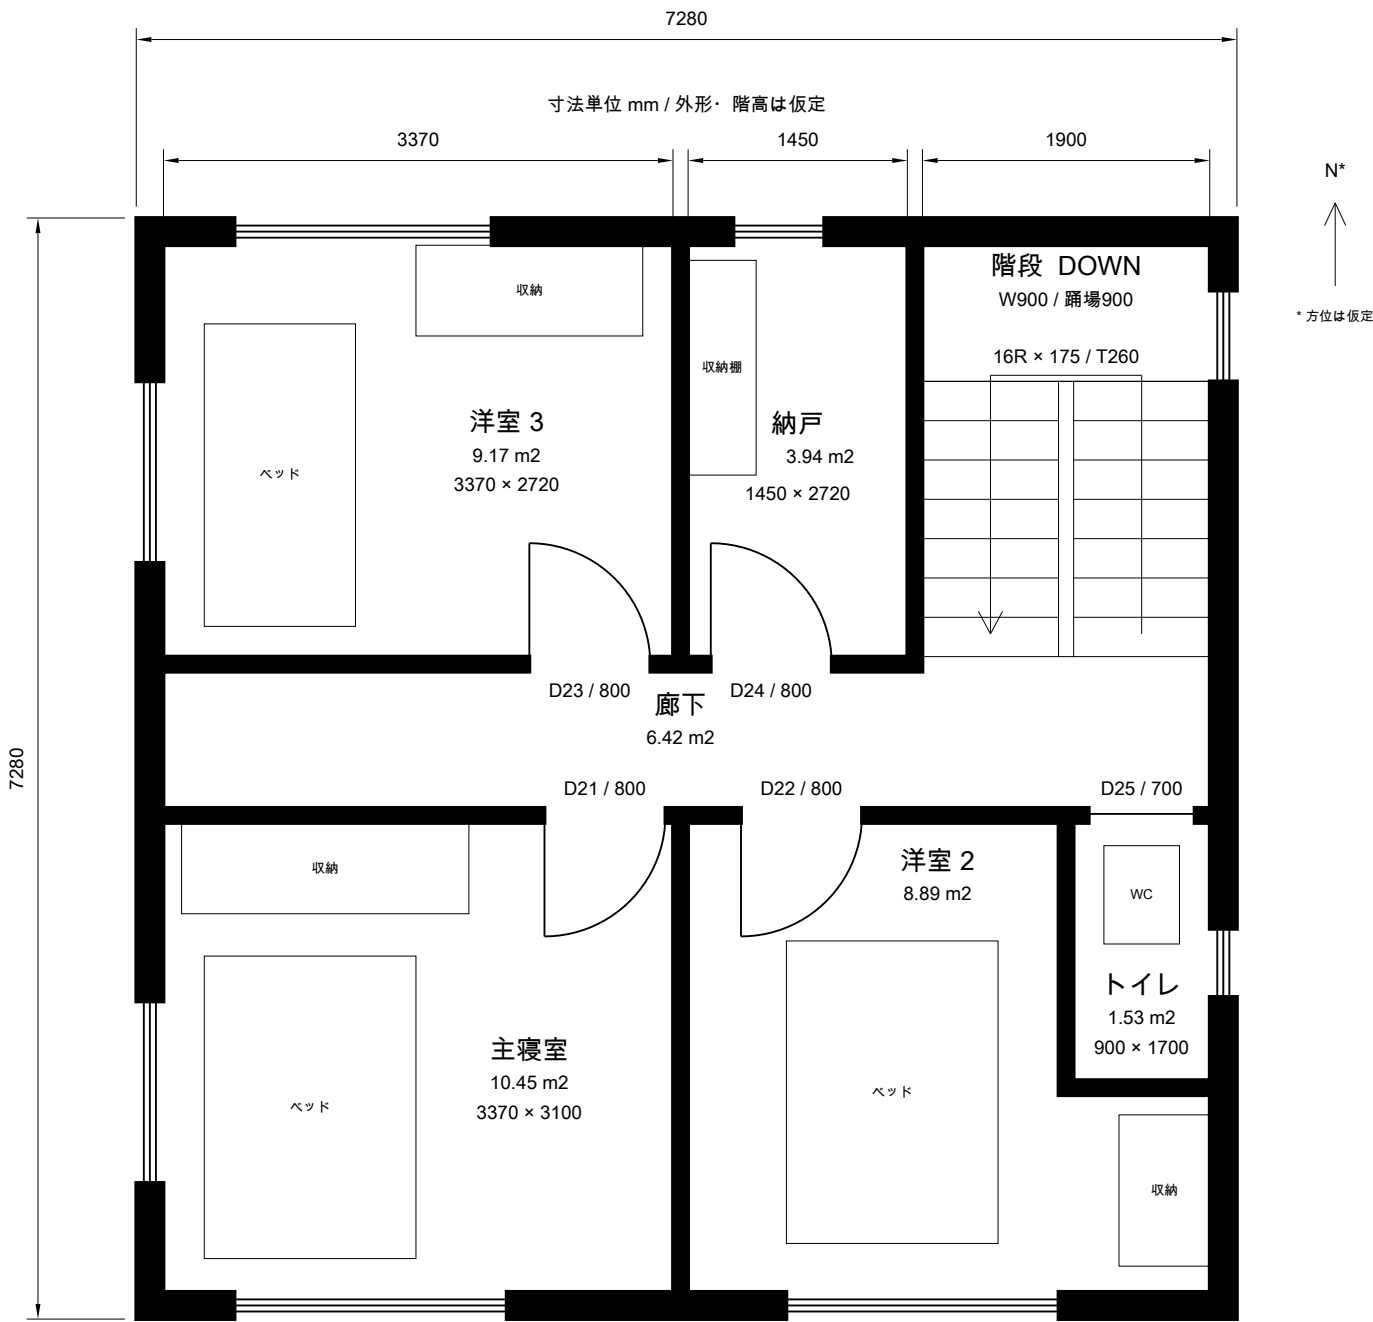

R02 / 2階 平面図 (参考計画)

室別面積表 (内法)

室名	面積 (m ²)
主寝室	10.45
洋室 2	8.89
洋室 3	9.17
納戸	3.94
トイレ	1.53
廊下	6.42
階段 (階段室)	5.17

注意事項・仮定条件

01. 建物外形 7,280×7,280、階高 2,800 mm はデモ用の仮定寸法。
02. 外壁 180、内壁 100 mm。家具・建具の寸法は計画上の仮定。
03. 方位と南側玄関は仮定。敷地・道路・配置条件は未設定。
04. 面積は壁内法の概算で家具占有分を含む。建築確認申請の面積ではない。
05. 廊下面積は階段を除く。階段面積は階段室の確保範囲を示す。
06. 階段：16R×175、T260、階段幅 900、踊場 900 mm。
07. 2階の階段室は床開口。踏板・手すりの詳細は別途設計。
08. 窓・扉は仮配置。引戸の戸袋・枠厚・製品仕様は未設計。
09. 便所：内法 900×1,700 mm。出入口 700 mm は枠厚を控除する前の寸法。
10. 構造・防火・耐震・法令適合は未検証。施工図として使用不可。
11. 東京都土木CAD製図基準 (令和6年4月) を住宅の図式に準用。
12. 既存 A3横・1:50 を継承。SXF電子納品は今回の対象外。

凡例

実線：壁・建具・家具の平面輪郭

寸法線：壁内法・建物外形・建具開口幅

D01 等：建具番号 UP：上り方向

北矢印：仮定方位 R02：製図様式改訂

施設名	住宅参考	
工事件名	日本一戸建て計画	
工事箇所	未定	
図面名称	2階平面図	
縮尺	1:50	図面番号
作製年月日	令和8年10月4日	002
事業所名 未定		全2枚