
東京スカイツリー / 基座平面図

LANDMARK-R05 | A3 | 1:500 | 単位 mm | 外観模式図

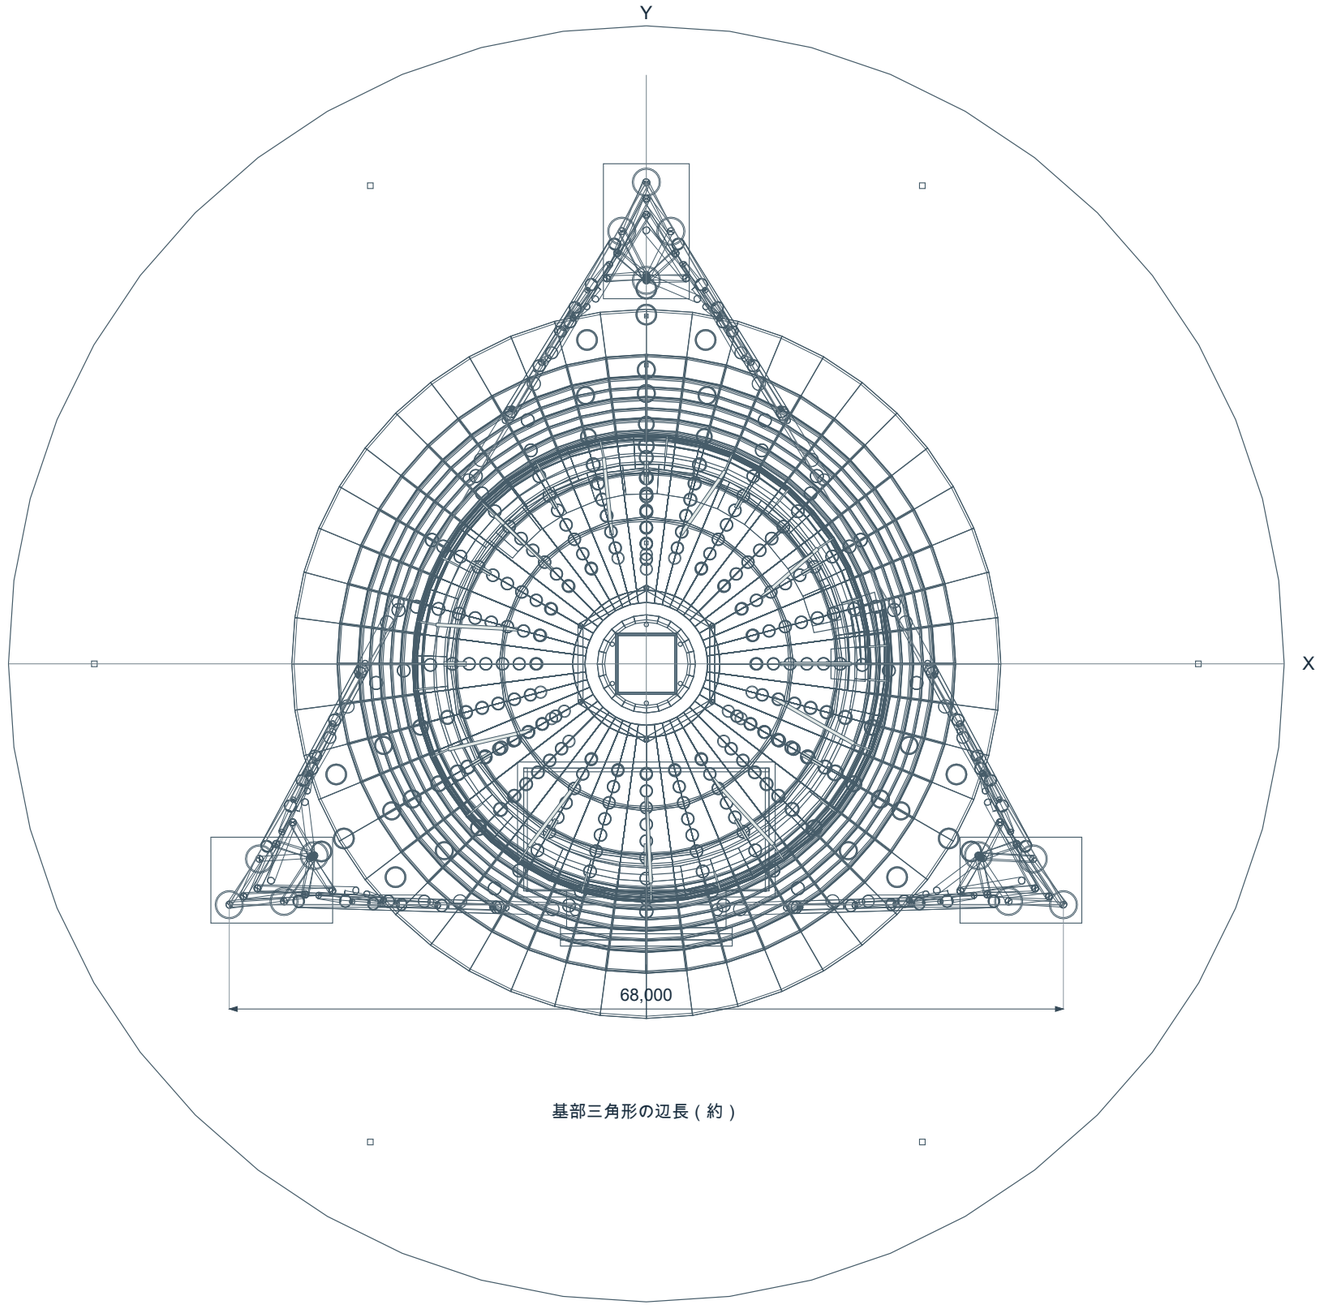

基部三角形の辺長 (約)

基座・足元 / 上部の投影外形を重ねた模式配置

方位はモデル軸のみ。実際の敷地方位・配置とは異なります。

モデル寸法と図面の対応

01 公式施設案内・公開資料の制御値

全高634,000 mm / 基部三角形の辺長約68,000 mm

地上315,000 mmで円形へ移行。

展望FL 340,000 / 345,000 / 350,000 mm

回廊445,000 / 450,000・最高451,200 mm

02 R05の外周鋼管・脚部3面の翼架構

隅部・面中央の円弧半径と輪郭24点は近似。

315 m/D32 → H495 m/D18の直錐はモデル仮定。

塔体H497 m / 約D6 mの六柱ゲイン塔を表現。

展望外壁の外傾71°を参考に外形を修正。

回廊外形・分節設備・TMD頂帽の細部は仮定。

03 展望床と設備屋上を区別

設備屋上375,000 mmは公表高度。外形断面は近似。

展望フロアの標高を375 mへ変更しない。

3組×4主柱から広がる翼架構と中央開口を保持。

外周水平材は中空円管。内部の角管とは区別。

翼の節点・管径・接合は実測復元ではない。

04 座標・データと参照

CADモデル空間は実寸1:1、単位mm。

平面X/Y・立面X/Zの正投影。方位はモデル用。

上部投影外形を基座平面に重ねて表示。

DXFの文字・寸法は編集可能。SVG/PDFは同じ投影。

公式 floor / about/spec/structure/ を参照。


未測量・未計算。測量図・構造図・施工図ではない。

text-CAD | LANDMARK-R05 | 2026-10-30

公表値を参照 / 未測量・未計算 / NOT FOR CONSTRUCTION

東京スカイツリー / 正立面図

LANDMARK-R05 | A3 | 1:3000 | 単位 mm | 外観模式図

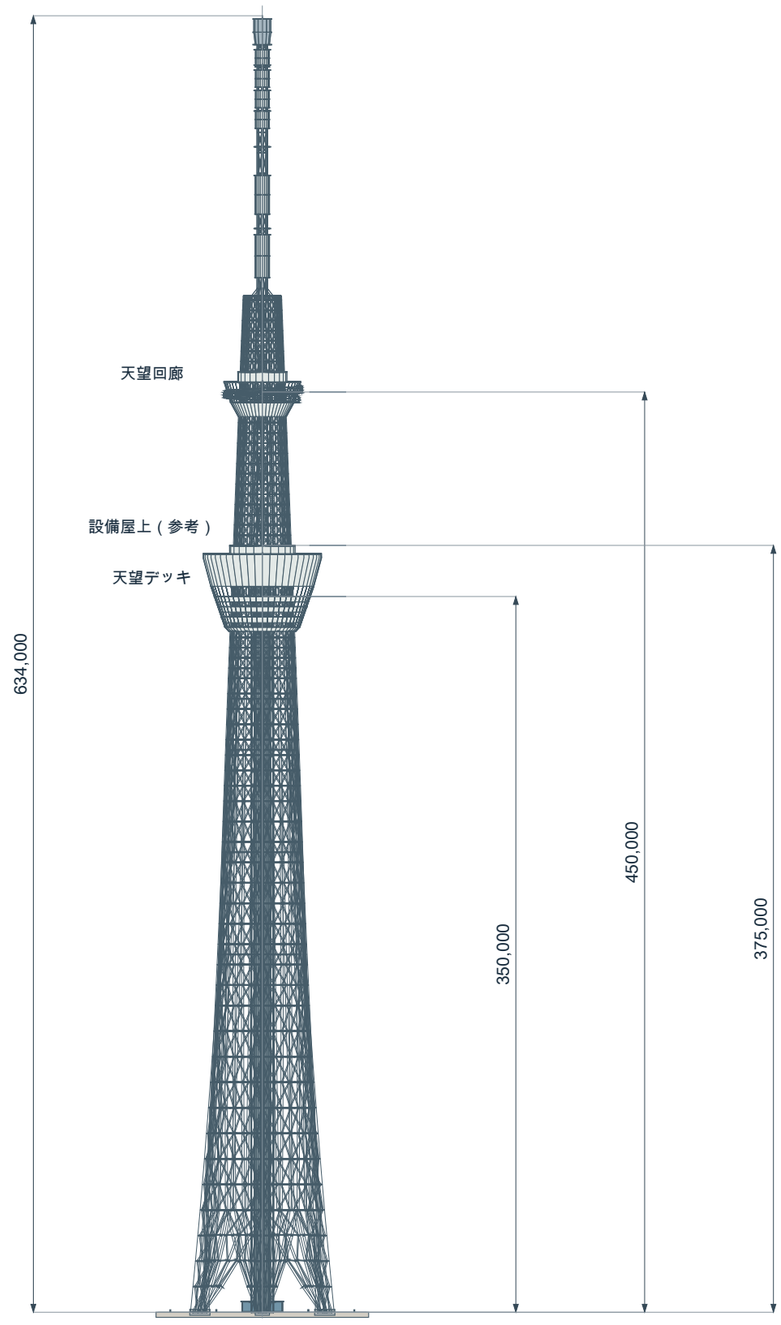

基準 GL ±0

正投影 / 展望施設の形状・鉄骨径は模式表現

公表値を参照 / 未測量・未計算 / NOT FOR CONSTRUCTION

モデル寸法と図面の対応


01 公式公表値 / 全高 634,000 mm

FL340/345/350 m・回廊445/450 m・最高451.2 m

315 m/D32 → H495 m/D18：直錐のモデル仮定。

塔体H497 m・ゲイン約D6 m・TMD頂帽は近似。


02 天望デッキ・設備冠 / 1:750

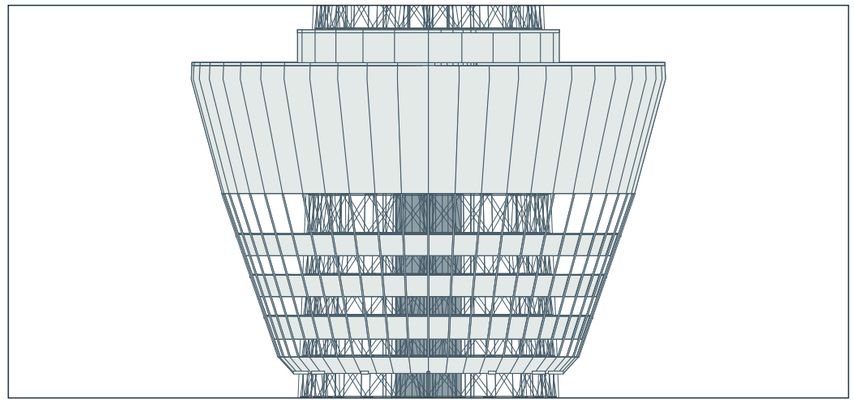

展望FL 340,000 / 345,000 / 350,000 mm

設備屋上375,000 mmは公表高度。展望床ではない。

03 天望回廊付近 / 1:500

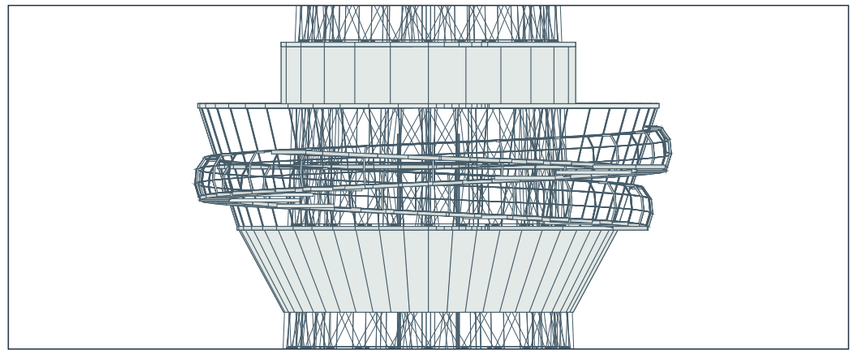

回廊445,000 → 450,000 / 最高451,200 mm

円弧・設備位置・外形細部は仮定。未測量・未計算。


text-CAD | LANDMARK-R05 | 2026-10-30

東京スカイツリー / 鋼管架構の構成

LANDMARK-R05 | A3 | モデル空間1:1 | 単位 mm | 外観模式図

公表値: 全高634,000 mm / 三脚の連結高さ約50m / 鋼管径・組幅・細部配置はモデル仮定。

鼎3組・3面の翼架構 / X-Z正投影 / 1:750

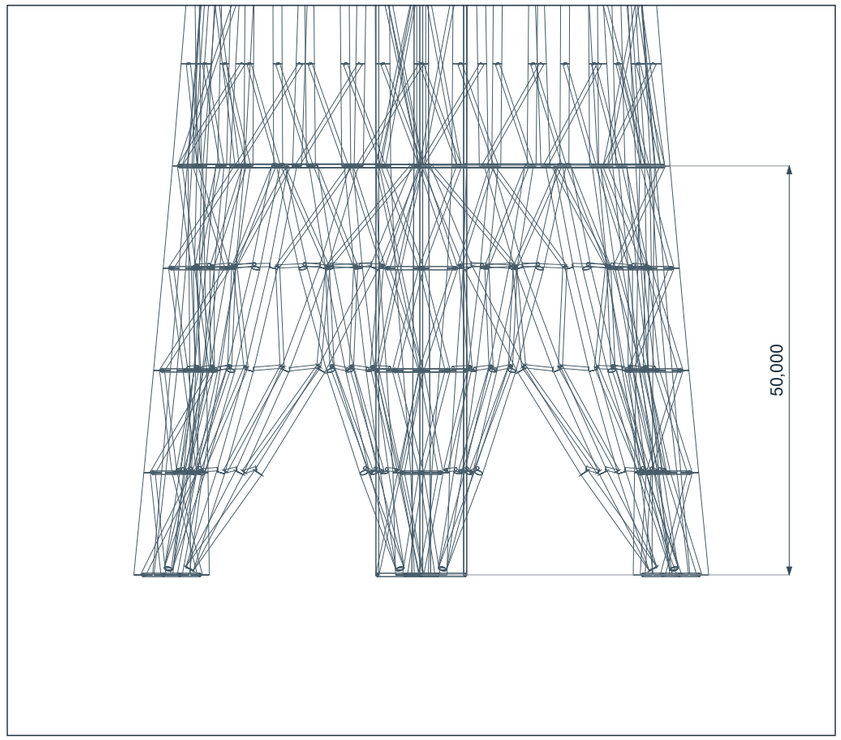

3組×4主柱。50,000はGL〜脚部連結帯の区間。

鼎トラス全体の高さを示す寸法ではない。

公式: リング12,500 / 水平連結25,000 mm。

翼は鼎主柱から展開。中央の開口は残す。

外周水平材は円管。STEPは真円中空。


心柱と鋼骨は別系統。制振性能は未解析。

参照: 公式構造案内（日建供図）・巴製作資料。

/about/spec/structure/ /steel-tower/works/skytree/

方位・断面位置はモデル参照。円周作図24点。

鼎1組・付随する翼架構 / 斜め正投影 / 1:200

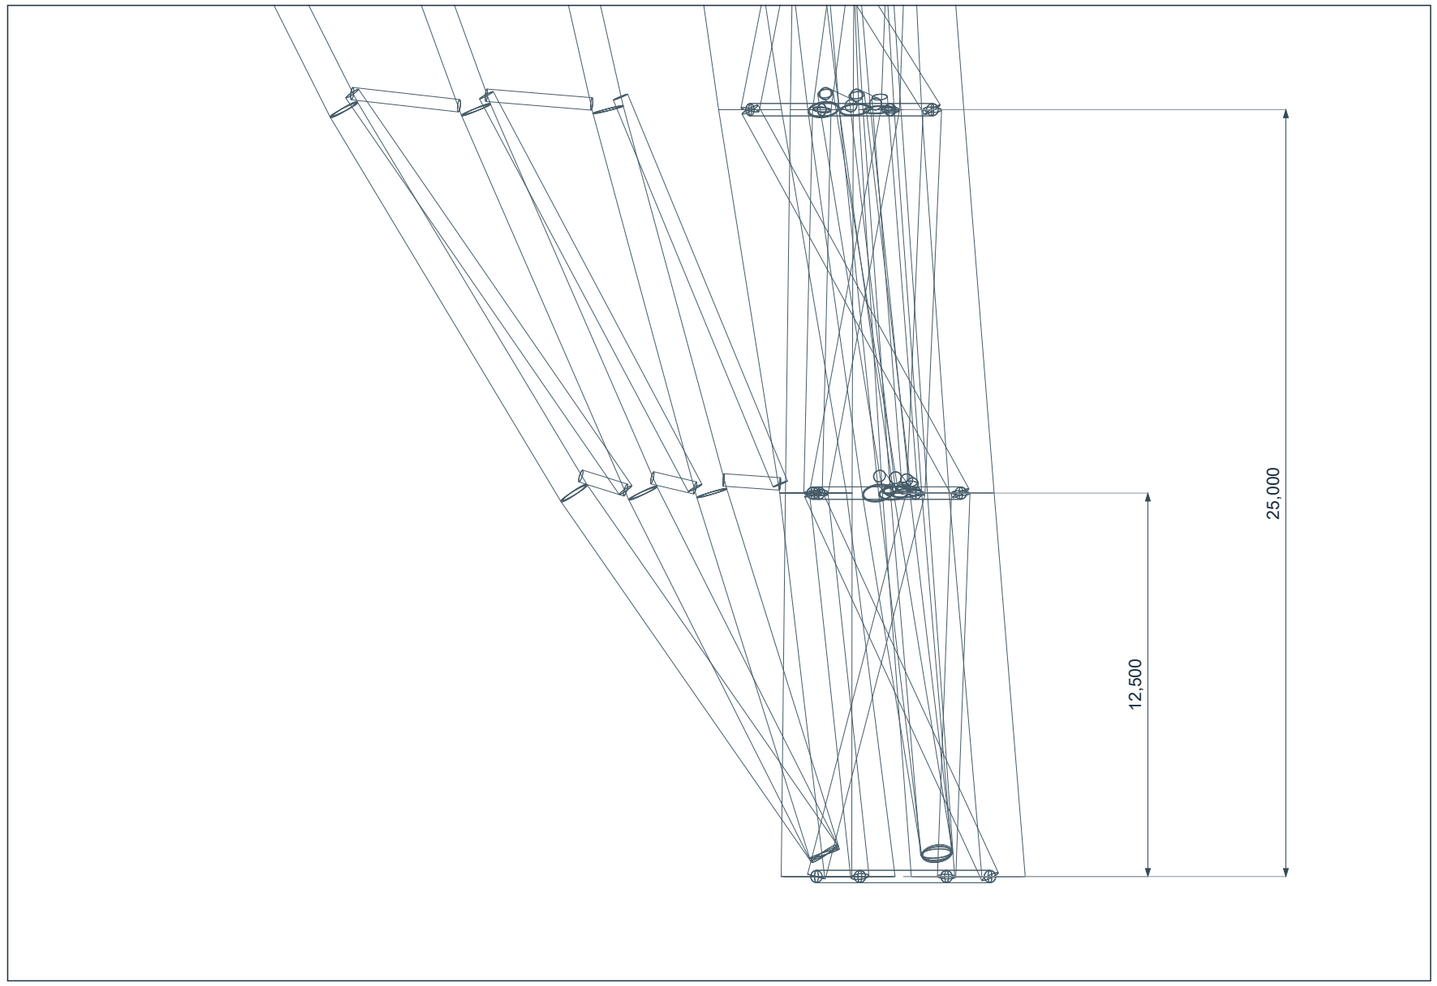

元のCAD部材を45°方向へ正投影。寸法は鉛直間隔。

接合は鋼管の直接分岐溶接を参考にした外観近似。

翼節点・管径・板厚・溶接は写真近似。原設計の復元ではない。

315 m以高は5,000 mm節間で近似。モデル仮定。

下部150/250 mの密度切替位置もモデル仮定。

未測量・未計算 / NOT FOR CONSTRUCTION / 構造耐力・溶接仕様を示す図ではありません。