
瀬戸大橋 / 南北備讃瀬戸大橋

BRIDGE-R03 | A3 | 1:10000 | 単位 mm | 外観参考図

橋梁全体平面図 / 橋軸X・横断Y

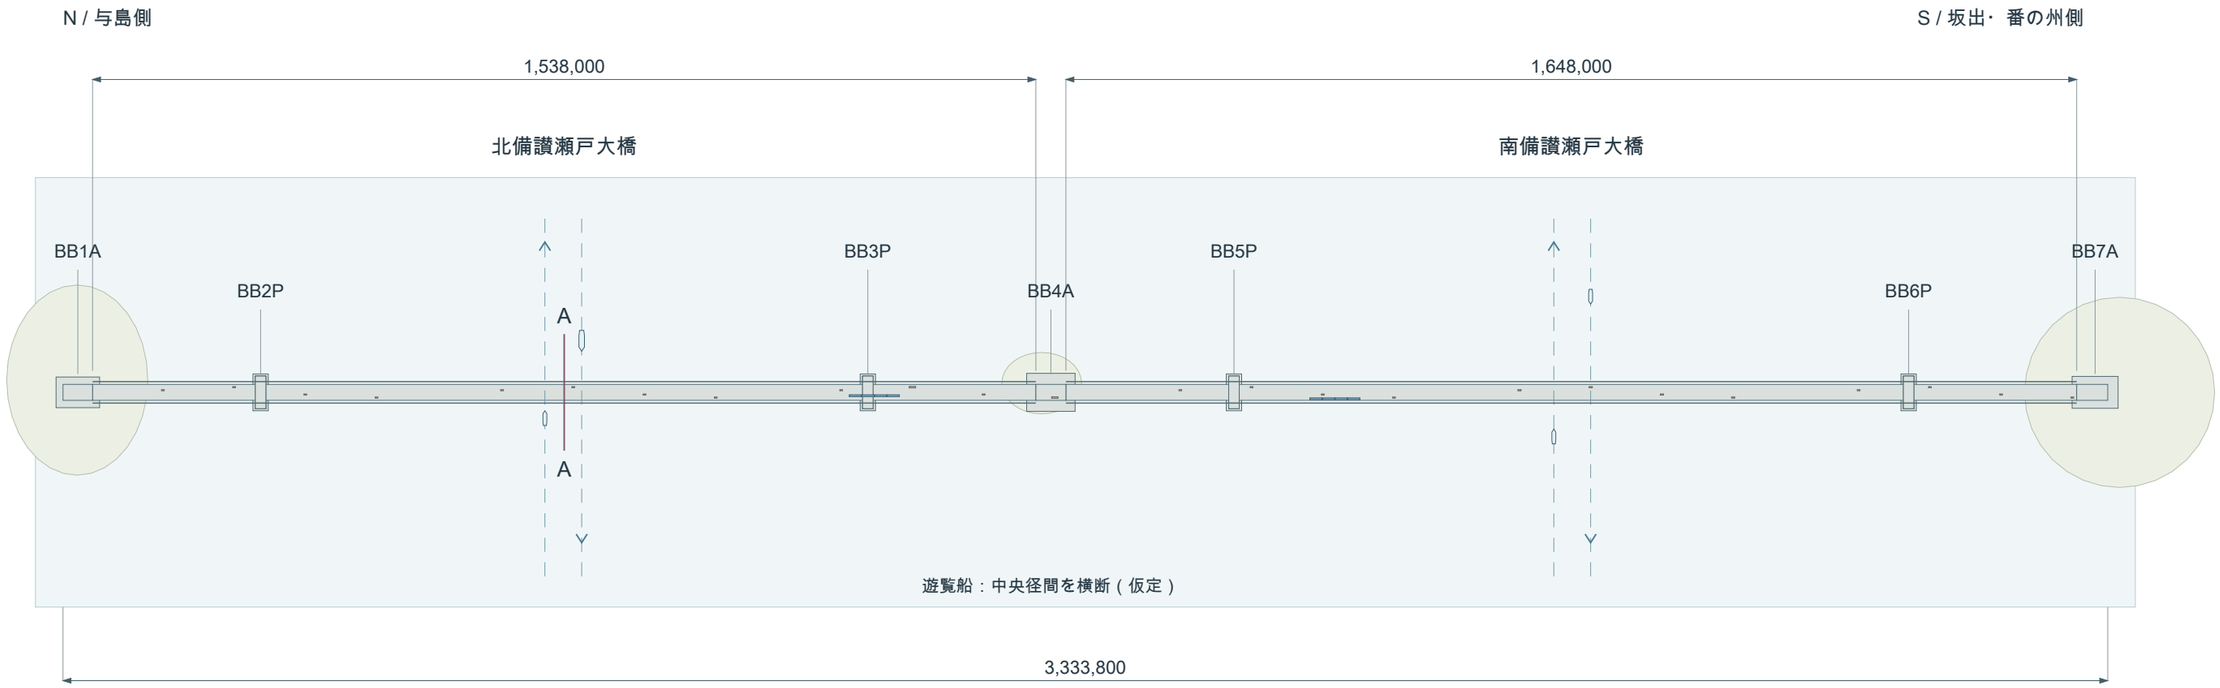

01 対象範囲と公表寸法

北：274,000 + 990,000 + 274,000 = 1,538,000 mm

南：274,000 + 1,100,000 + 274,000 = 1,648,000 mm

BB4Aは一つの共用アンカレイジ。接続区間は49,000 mm。


橋端間3,333,800 mm：公表区間1611+1723 mとの丸め差。

A-A：北橋中央径間。下層電車は4両×2編成を投影表示。


参照：JB本四高速 / 川崎製鉄技報。自動車24台・遊覧船4隻・電車2編成は説明用の配置。

車・船・電車はt=0の静止位置。経路・速度は説明用の仮定。

車両（1:100）

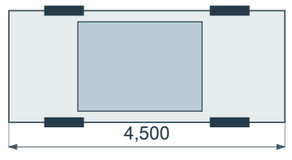

遊覧船（1:500）

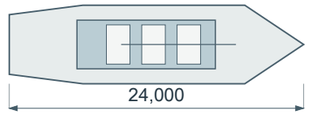


車体・船体・速度・配置は説明用の仮定。Webのみ移動し、CADは静止。

公表値と実景を参照 / 未測量・未計算 / NOT FOR CONSTRUCTION

text-CAD 2026-11-07 PLAN

瀬戸大橋 / 南北備讃瀬戸大橋

橋梁全体側面図 / 水平・鉛直とも1:10000 (鉛直倍率なし)

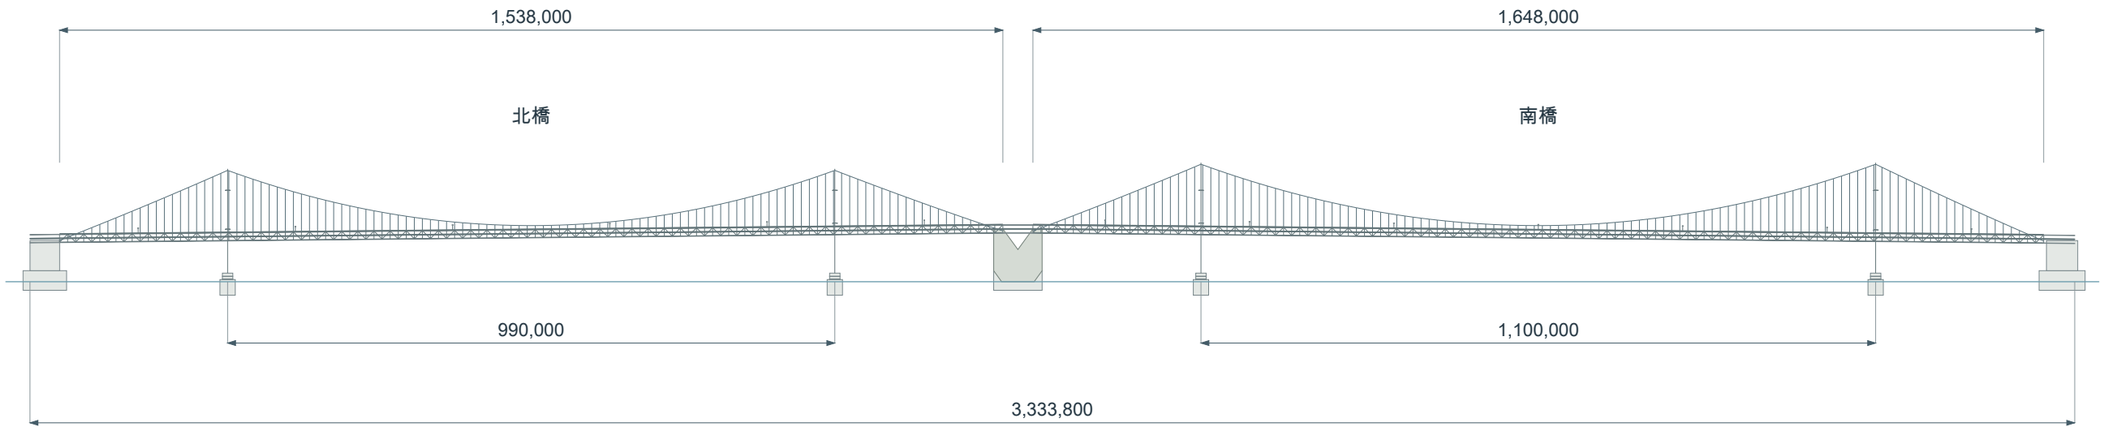

全体側面図：模型の橋面はBB4Aから両側へ約1%低下。北側勾配は南側の対称仮定。

公式の支配寸法

北橋・中央径間	990,000 mm
南橋・中央径間	1,100,000 mm
北橋・主塔頂高	T.P. +184,000 mm
南橋・主塔頂高	T.P. +194,000 mm
北橋・主ケーブル径	998 mm (被覆を除く)
南橋・主ケーブル径	1,062 mm (被覆を除く)

標高・写真合わせの注意

T.P.は東京湾平均海面基準。モデル海面はT.P.0の仮定。

公表の航路高65mは略最高高潮面からの値。

その値をモデルの海面からの高さへ直接置換しない。

BB4Aの93m道路高を起点に縦断を簡略化。


主塔の横構・ケーブル曲線・基礎深さは外観近似。

等縮尺のため桁高は小さく見える。第3図で詳細確認。

参照：JB本四高速公式側面図 / 本四公団・コンクリート工学 Vol.22 No.11 (1984)

瀬戸大橋 / 南北備讃瀬戸大橋

A-A 横断面 1:250 / BB4A通過部 1:750 / 軌頂詳細 1:20

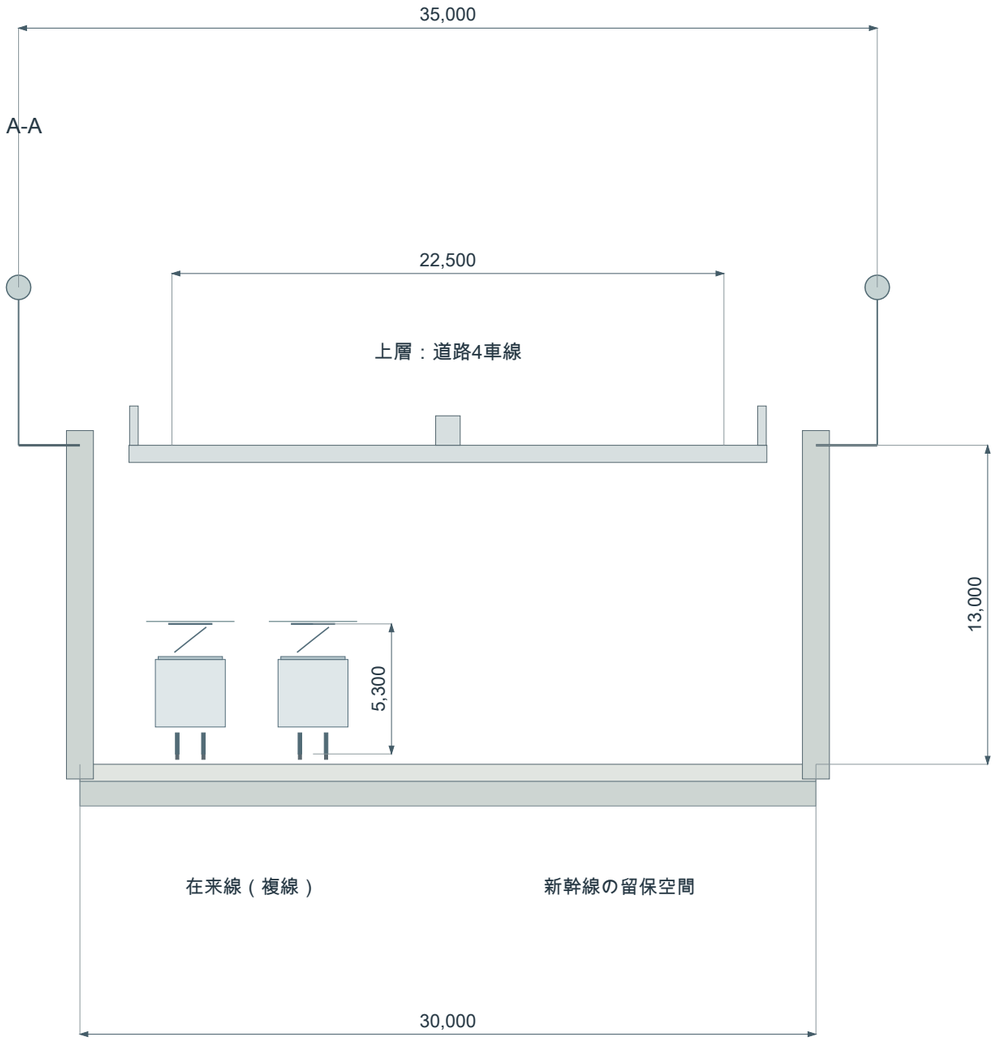

断面 X=-793,500 mm / 北橋中央径間

上層 T.P.+85,065 / 下層 T.P.+72,065 mm（近似）

車両高5,300・架線高5,400 mmは軌頂からの仮定。


横桁を1,200 mm下げ、車輪との干渉を解消。

公表値：主桁間30m・桁高13m・ケーブル間35m。


車両限界・動揺・電気離隔の法定照査は未実施。

BB4A：下層鉄道の通過断面

通行有効高さ 11,880 mm（仮定）

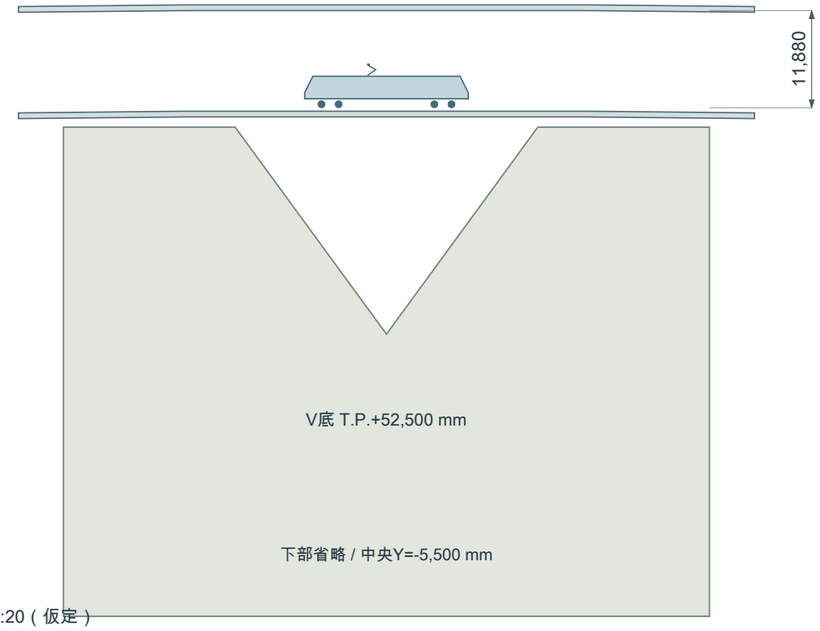

軌頂詳細 1:20（仮定）

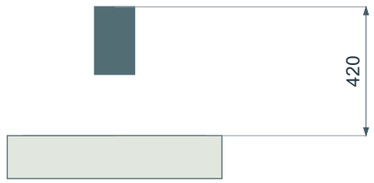

寸法はレール頂と下層床上面との差。

開口は説明用の仮定。

原図のアンカレイジを

再現する施工図ではない。

実際の経路・地盤・安全性を保証する断面図ではない。