


R09 平面草案 / 1階 / 3LDK + 物干しバルコニー

演示方案・未承認 / CONCEPT DRAFT / 2026-10-07 / A3 1:50 / mm

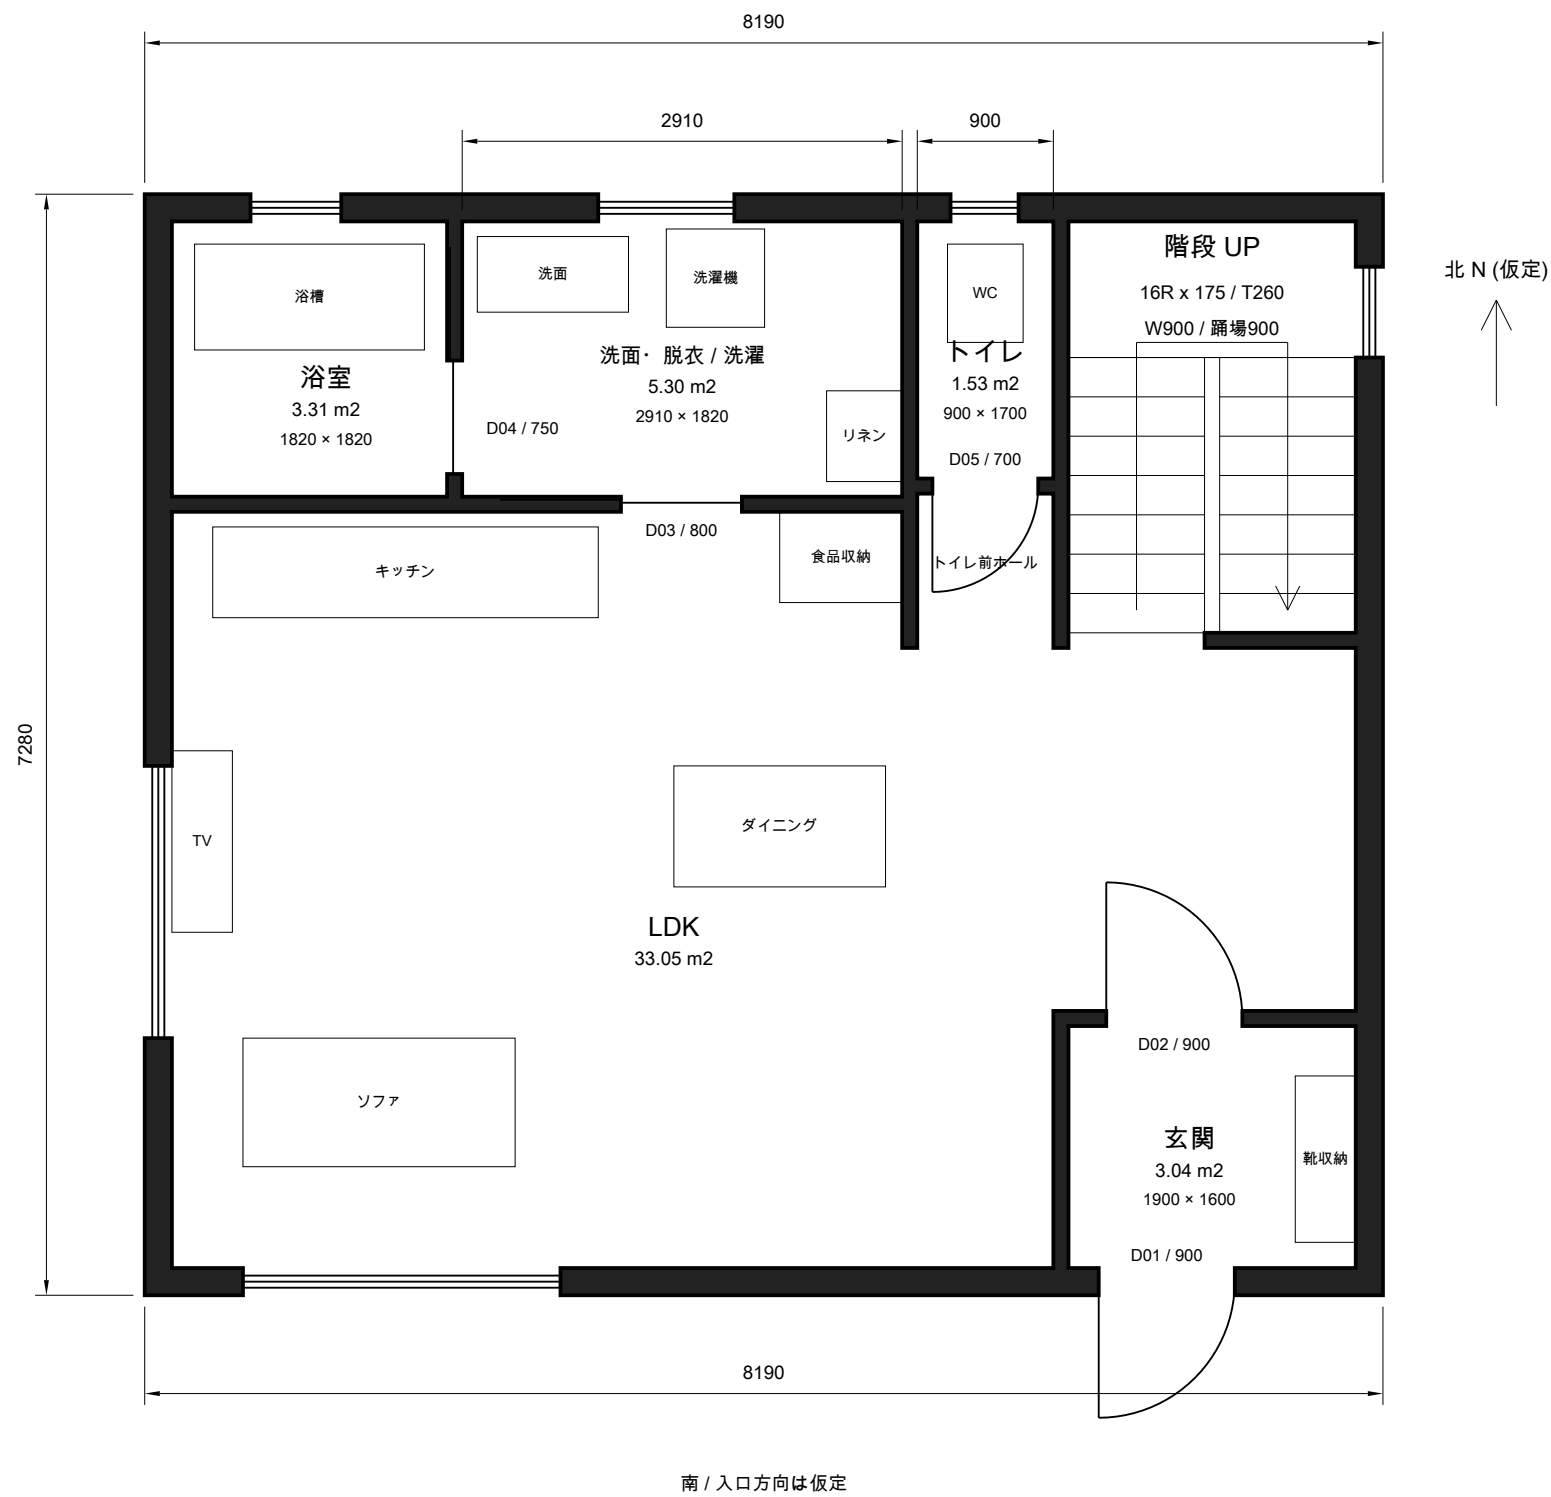

R09 平面草案 / 2階 / 3LDK + 物干しバルコニー

演示方案・ 未承認 / CONCEPT DRAFT / 2026-10-07 / A3 1:50 / mm



主要変更 / 主要修改

外形 8190 x 7280 / 階高 2800 (仮定)

旧外形 7280 x 7280 → 東側 +910

一階 LDK と玄関の長い隔壁を解消

トイレを階段横へ移動・ 上下階一致

便所自体を無理に縮小しない

バルコニーは共用通路から出入り

個室を通らず物干し可能

バルコニー外形 3640 x 1500 (仮定)

手摺内側 3440 x 1400 / 4.82 m²

室面積 / 牆内几何面積 (家具含む)

主寝室	9.61 m ²
収納	2.79 m ²
洋室 2	11.25 m ²
洋室 3	13.14 m ²
ホール / 物干し通路	7.05 m ²
トイレ	1.53 m ²
トイレ前ホール	0.83 m ²
階段	5.17 m ²
バルコニー	4.82 m ²

確認待ち / 待核定

梁・柱・耐力壁・基礎を再設計する。

既存 W/S/RC・都市別案は適用しない。

採光・換気・防火・敷地・設備は未検証。

階段の床開口・梁下高さは未検証。

バルコニー支持・防水・排水・手摺は未設計。

室面積は法定床面積ではない。

外形矩形: 59.62 m²/階; 2階分 119.25 m²。

別途バルコニー外形 5.46 m²。

現行の承認済み3Dモデルは保持。