


外構・基礎 補足計画図 / R09


単位 mm / 配置 1:100 / A3 / 全寸法・方位・敷地はデモ仮定 / 2026-10-07

01 配置図

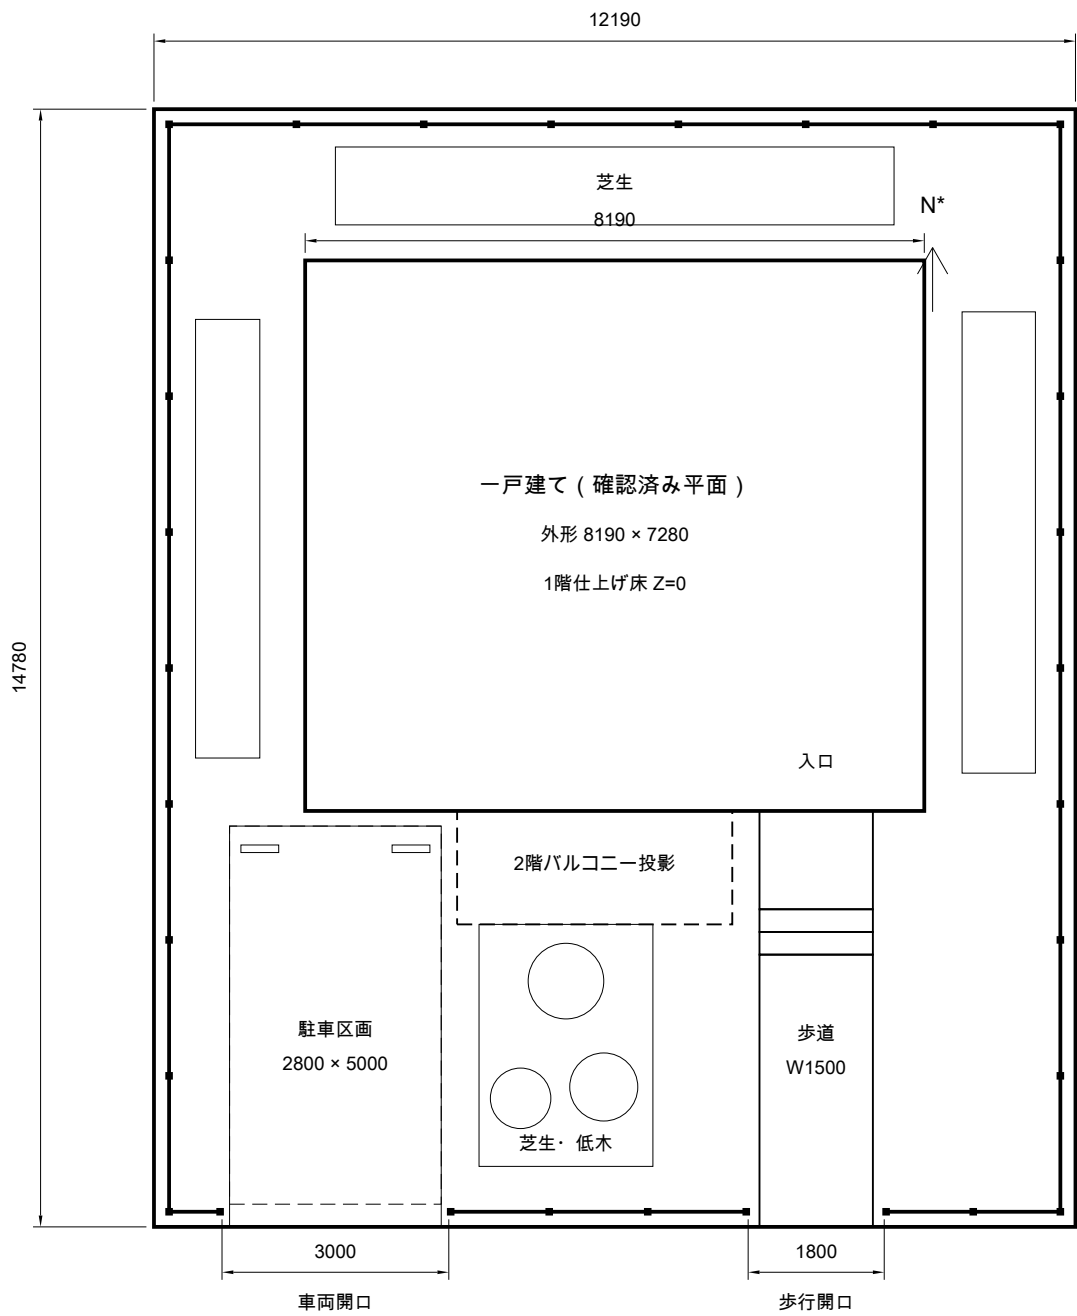

敷地外形 180.1682 m² (幾何面積)
南側アクセスを仮定 / 道路・境界条件は未確定

02 基礎参考断面 / 1:25 (模式図)

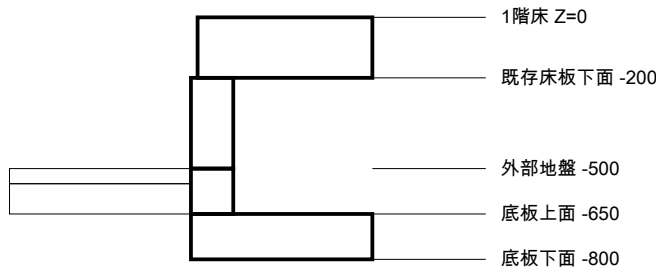

底板厚150 / 立上り幅140 (仮定)
フェンス基礎 : 300角 / Z=-950 ~ -550
地盤面からフェンス天端まで1200

03 玄関への高さ関係 (模式・縮尺なし)

地盤 -500 → 追加段 -330 → 既存段 -160
→ 既存ポーチ -25 → 玄関床 0
段差 : 170 / 170 / 135 / 25
追加段・歩道幅1500 / 追加段奥行300

04 計画の前提

敷地・駐車場・地盤は仮定。無舗装部は砂利。
南側に車両3000・歩行1800の実開口を確保。
フェンス29面・柱31本。横桟間の隙間40。
基礎・庭・フェンスは独立した表示グループ。
確認済み1・2階平面と小屋裏形状を保持。
地盤調査・配筋・耐力・排水・車両軌跡は未設計。
境界・道路・植栽選定・法規は実計画で要検討。
本図は施工図・構造計算・測量図ではない。

text-CAD / R09-SITE / 参考デモ