



外構・基礎 補足計画図 / R14

単位 mm / 配置 1:100 / A3 / 全寸法・方位・敷地はデモ仮定 / 2026-10-07

01 配置図

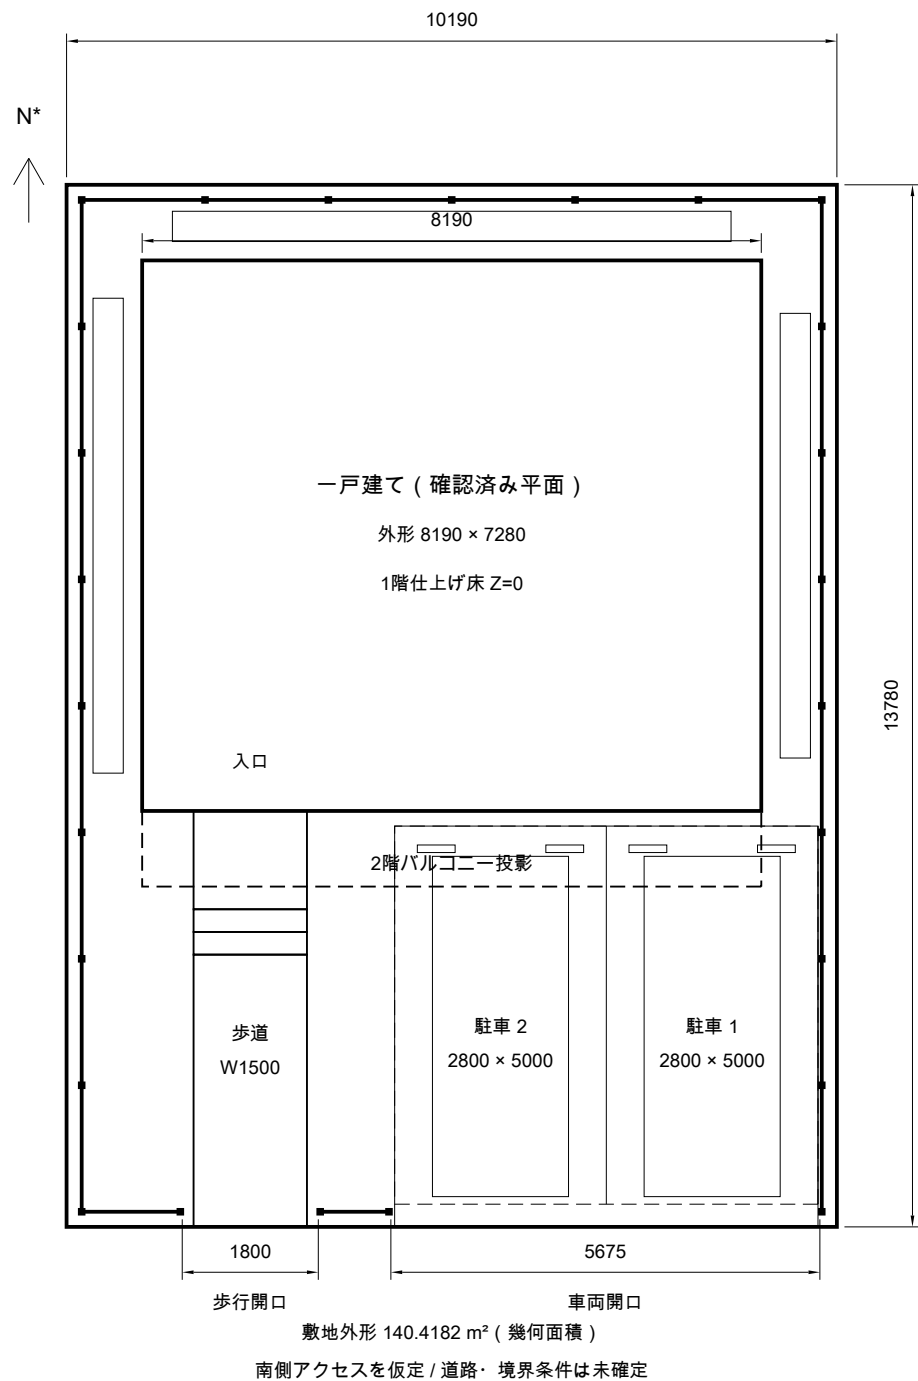

02 基礎参考断面 / 1:25 (模式図)

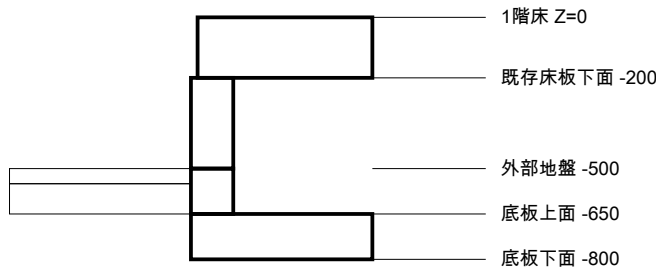

底板厚150 / 立上り幅140 (仮定)

フェンス基礎 : 300角 / Z=-950 ~ -550

地盤面からフェンス天端まで1200

03 玄関への高さ関係 (模式・縮尺なし)

地盤 -500 → 追加段 -330 → 既存段 -160

→ 既存ポーチ -25 → 玄関床 0

段差 : 170 / 170 / 135 / 25

追加段・歩道幅1500 / 追加段奥行300

04 計画の前提

敷地・駐車場・地盤は仮定。無舗装部は砂利。

並列2台 : 各2800×5000。車両開口5675。

フェンス24面・柱26本。横桟間の隙間40。

東・西・北の余白1000、南5500 (仮定)。

室内・小屋裏は保持。陽台奥行1000、柱なし。

地盤調査・配筋・耐力・排水・車両軌跡は未設計。

玄関ポーチ先端300は陽台の外 (仮定)。

本図は施工図・構造計算・測量図ではない。