# 1階平面図




南 / 入口方向は仮定

## 室別面積表（内法）

| 室名 | 面積（m²） |
|---|---|
| LDK | 33.95 |
| 玄関 | 3.04 |
| 浴室 | 3.31 |
| 洗面・脱衣 / 洗濯 | 5.30 |
| トイレ | 1.64 |
| 階段（階段室） | 3.53 |
| 階段下収納 | 1.41 |

## 注意事項・仮定条件

01. 建物外形 8,190×7,280、階高 2,800 mm はデモ用の仮定寸法。
02. 外壁 180、内壁 100 mm。家具・建具の寸法は計画上の仮定。
03. R22：寝室引戸は閉位置、両階洗面は600×450。浴槽は東西壁間、シャワーは東壁南寄り。
04. 面積は壁内法の概算で家具占有分を含む。建築確認申請の面積ではない。
05. 廊下面積は階段を除く。階段面積は階段室の確保範囲を示す。
06. 階段：16R×175、T260、階段幅 900、踊場 900 mm。
07. 対面キッチン2550×650・背面通路900。小屋裏北側換気窓2枚各200×450は仮定。
08. 南LDK窓H2200、2寝室は引違い戸H2100。ガラス・防水・耐力は未設計。
09. 便所：内法 900×1,820 mm。出入口 700 mm は枠厚を控除する前の寸法。
10. 構造・防火・耐震・法令適合は未検証。施工図として使用不可。
11. 東京都土木CAD製図基準（令和6年4月）を住宅の図式に準用。
12. 南側バルコニー8190×1000は仮定。柱なし・ポーチ先端300露出。耐力・防水・排水は未設計。

## 凡例

実線：壁・建具・家具の平面輪郭


寸法線：壁内法・建物外形・建具開口幅

D01 等：建具番号　UP：上り方向

北矢印：仮定方位　R22：左右反転・対面キッチン・北側換気窓・構造未計算

| | | |
|---|---|---|
| 施設名 | 住宅参考 | |
| 工事件名 | 日本一戸建て計画 | |
| 工事箇所 | 未定 | |
| 図面名称 | 1階平面図 | |
| 縮尺 | 1:50 | 図面番号 001 全2枚 |
| 作製年月日 | 令和8年10月7日 | |
| 事業所名　未定 | | |

# 2階平面図

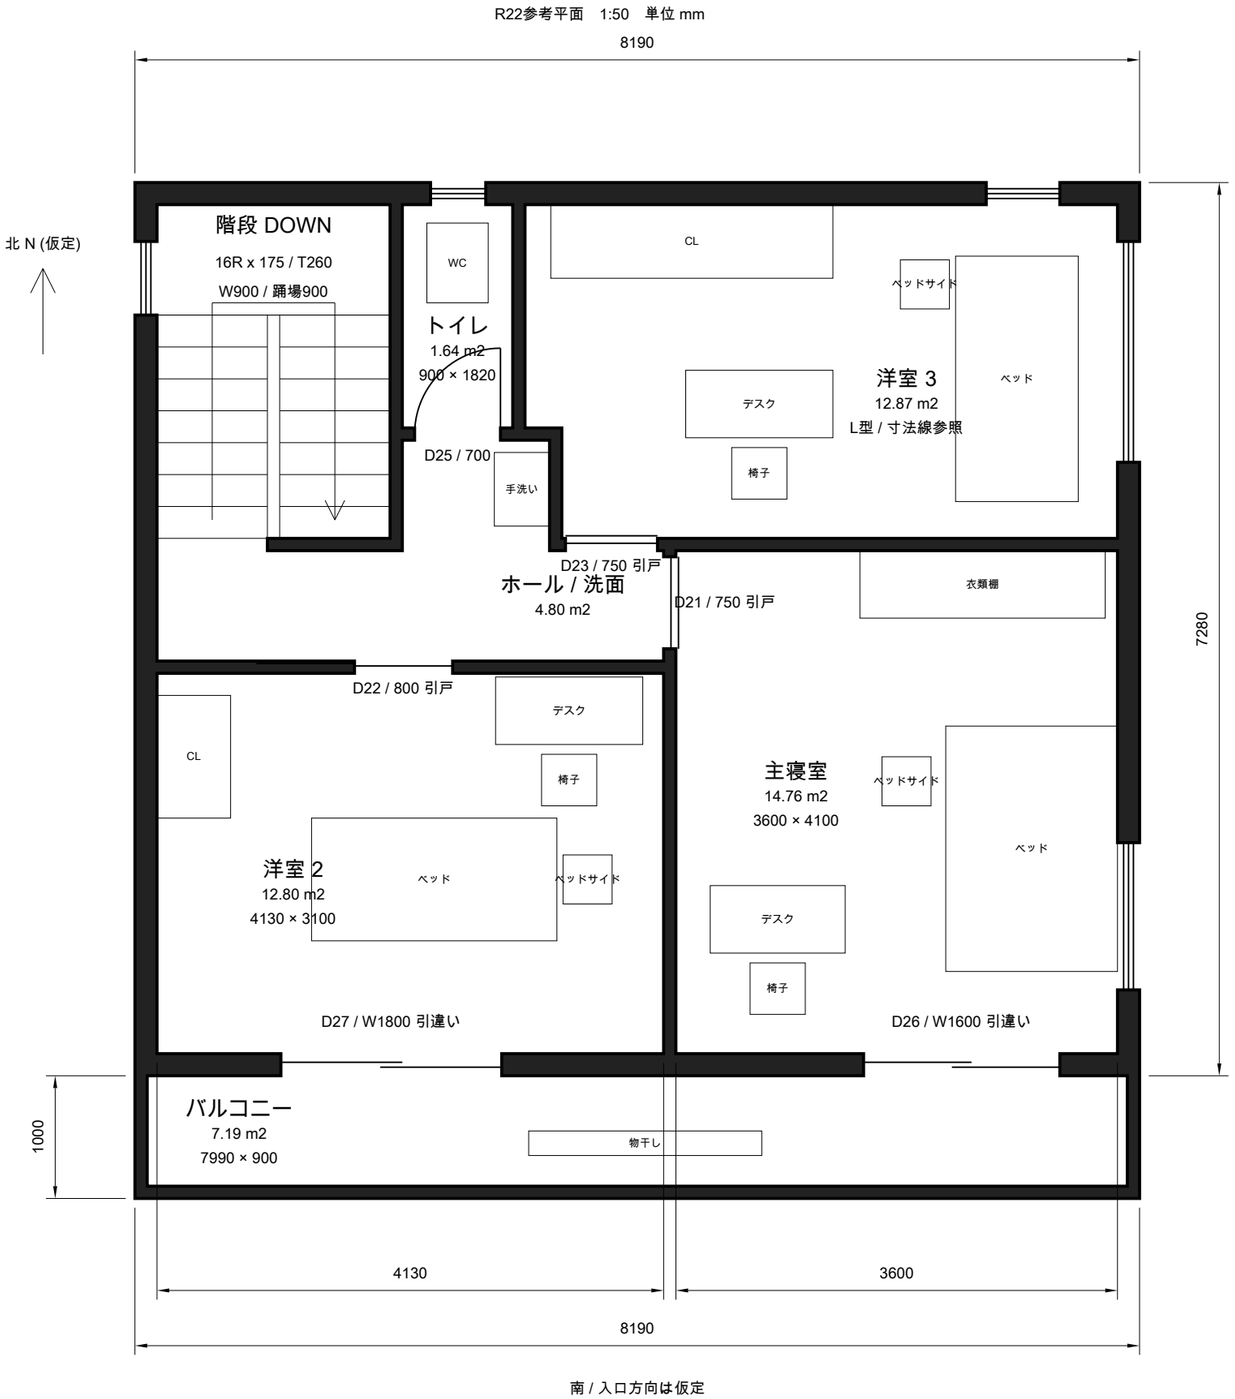


## 室別面積表（内法）

| 室名 | 面積（m²） |
|---|---|
| 主寝室 | 14.76 |
| 洋室 2 | 12.80 |
| 洋室 3 | 12.87 |
| ホール / 洗面 | 4.80 |
| トイレ | 1.64 |
| 階段（階段室） | 5.17 |
| バルコニー | 7.19 |

## 注意事項・仮定条件

01. 建物外形 8,190×7,280、階高 2,800 mm はデモ用の仮定寸法。
02. 外壁 180、内壁 100 mm。家具・建具の寸法は計画上の仮定。
03. R22：寝室引戸は閉位置、両階洗面は600×450。浴槽は東西壁間、シャワーは東壁南寄り。
04. 面積は壁内法の概算で家具占有分を含む。建築確認申請の面積ではない。
05. 廊下面積は階段を除く。階段面積は階段室の確保範囲を示す。
06. 階段：16R×175、T260、階段幅 900、踊場 900 mm。
07. 対面キッチン2550×650・背面通路900。小屋裏北側換気窓2枚各200×450は仮定。
08. 南LDK窓H2200、2寝室は引違い戸H2100。ガラス・防水・耐力は未設計。
09. 便所：内法 900×1,820 mm。出入口 700 mm は枠厚を控除する前の寸法。
10. 構造・防火・耐震・法令適合は未検証。施工図として使用不可。
11. 東京都土木CAD製図基準（令和6年4月）を住宅の図式に準用。
12. 南側バルコニー8190×1000は仮定。柱なし・ポーチ先端300露出。耐力・防水・排水は未設計。

## 凡例

実線：壁・建具・家具の平面輪郭

寸法線：壁内法・建物外形・建具開口幅

D01 等：建具番号　UP：上り方向

北矢印：仮定方位　R22：左右反転・対面キッチン・北側換気窓・構造未計算

| | | |
|---|---|---|
| 施設名 | 住宅参考 | |
| 工事件名 | 日本一戸建て計画 | |
| 工事箇所 | 未定 | |
| 図面名称 | 2階平面図 | |
| 縮尺 | 1:50 | 図面番号 |
| 作製年月日 | 令和8年10月7日 | 002 |
| 事業所名　未定 | | 全2枚 |