



小屋裏収納 補足計画図 / R10

単位 mm / A3・ 1:50 / 全寸法はデモ仮定 / 2026-10-07

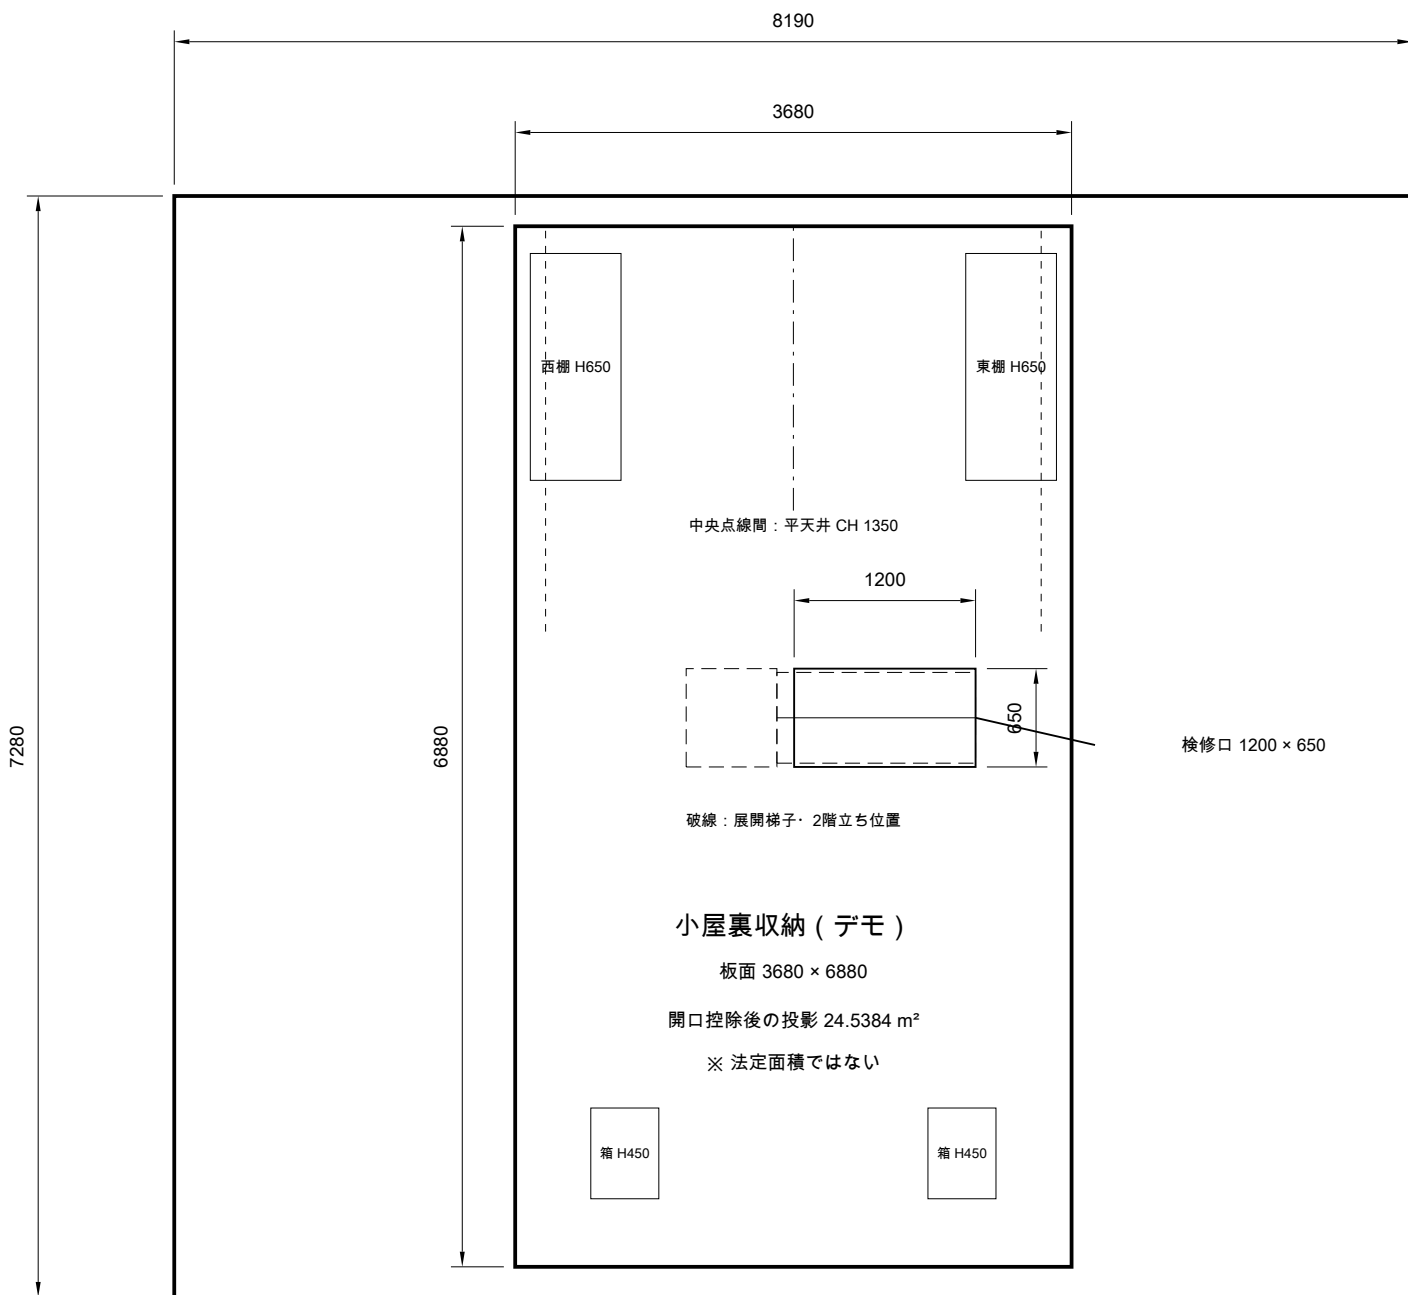

参考断面 (東西・ Y=2000) / 屋根外形維持

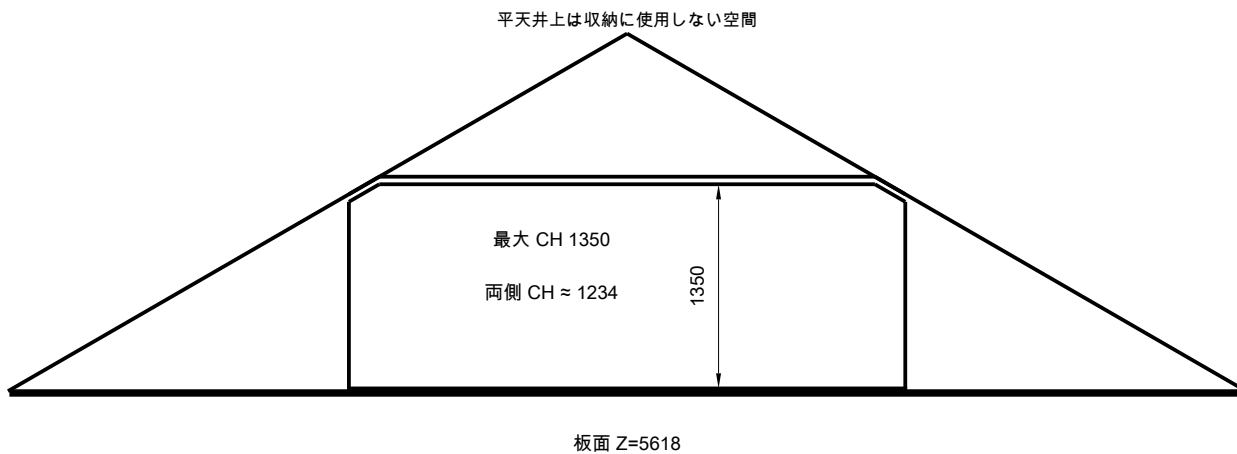

所在地未定の収納デモ。法規適合の確定ではない。

R10確認済み平面・ 屋根外形と整合。

CH：板面から実体天井まで。上限1350は仮定。

床基板24・ 仕上18・ 平天井厚50は仮定寸法。

検修梯子：幅600・ 65°・ 高さ2818・ 踏板10枚。

2階廊下に展開。展開中は通行を占有する。

上端立位 最低CH約1254。収納用の検修アクセス。

木構部材は概念表示。耐荷重・ 接合は未検証。

実製品・ 安全操作・ 断熱換気・ 法規は要確認。

R10平面の公共廊下上に検修口を配置。